LOT 1.1:I.3 AMPHITHEATRE DE 350 PLACES (SALLE DES ACTES)

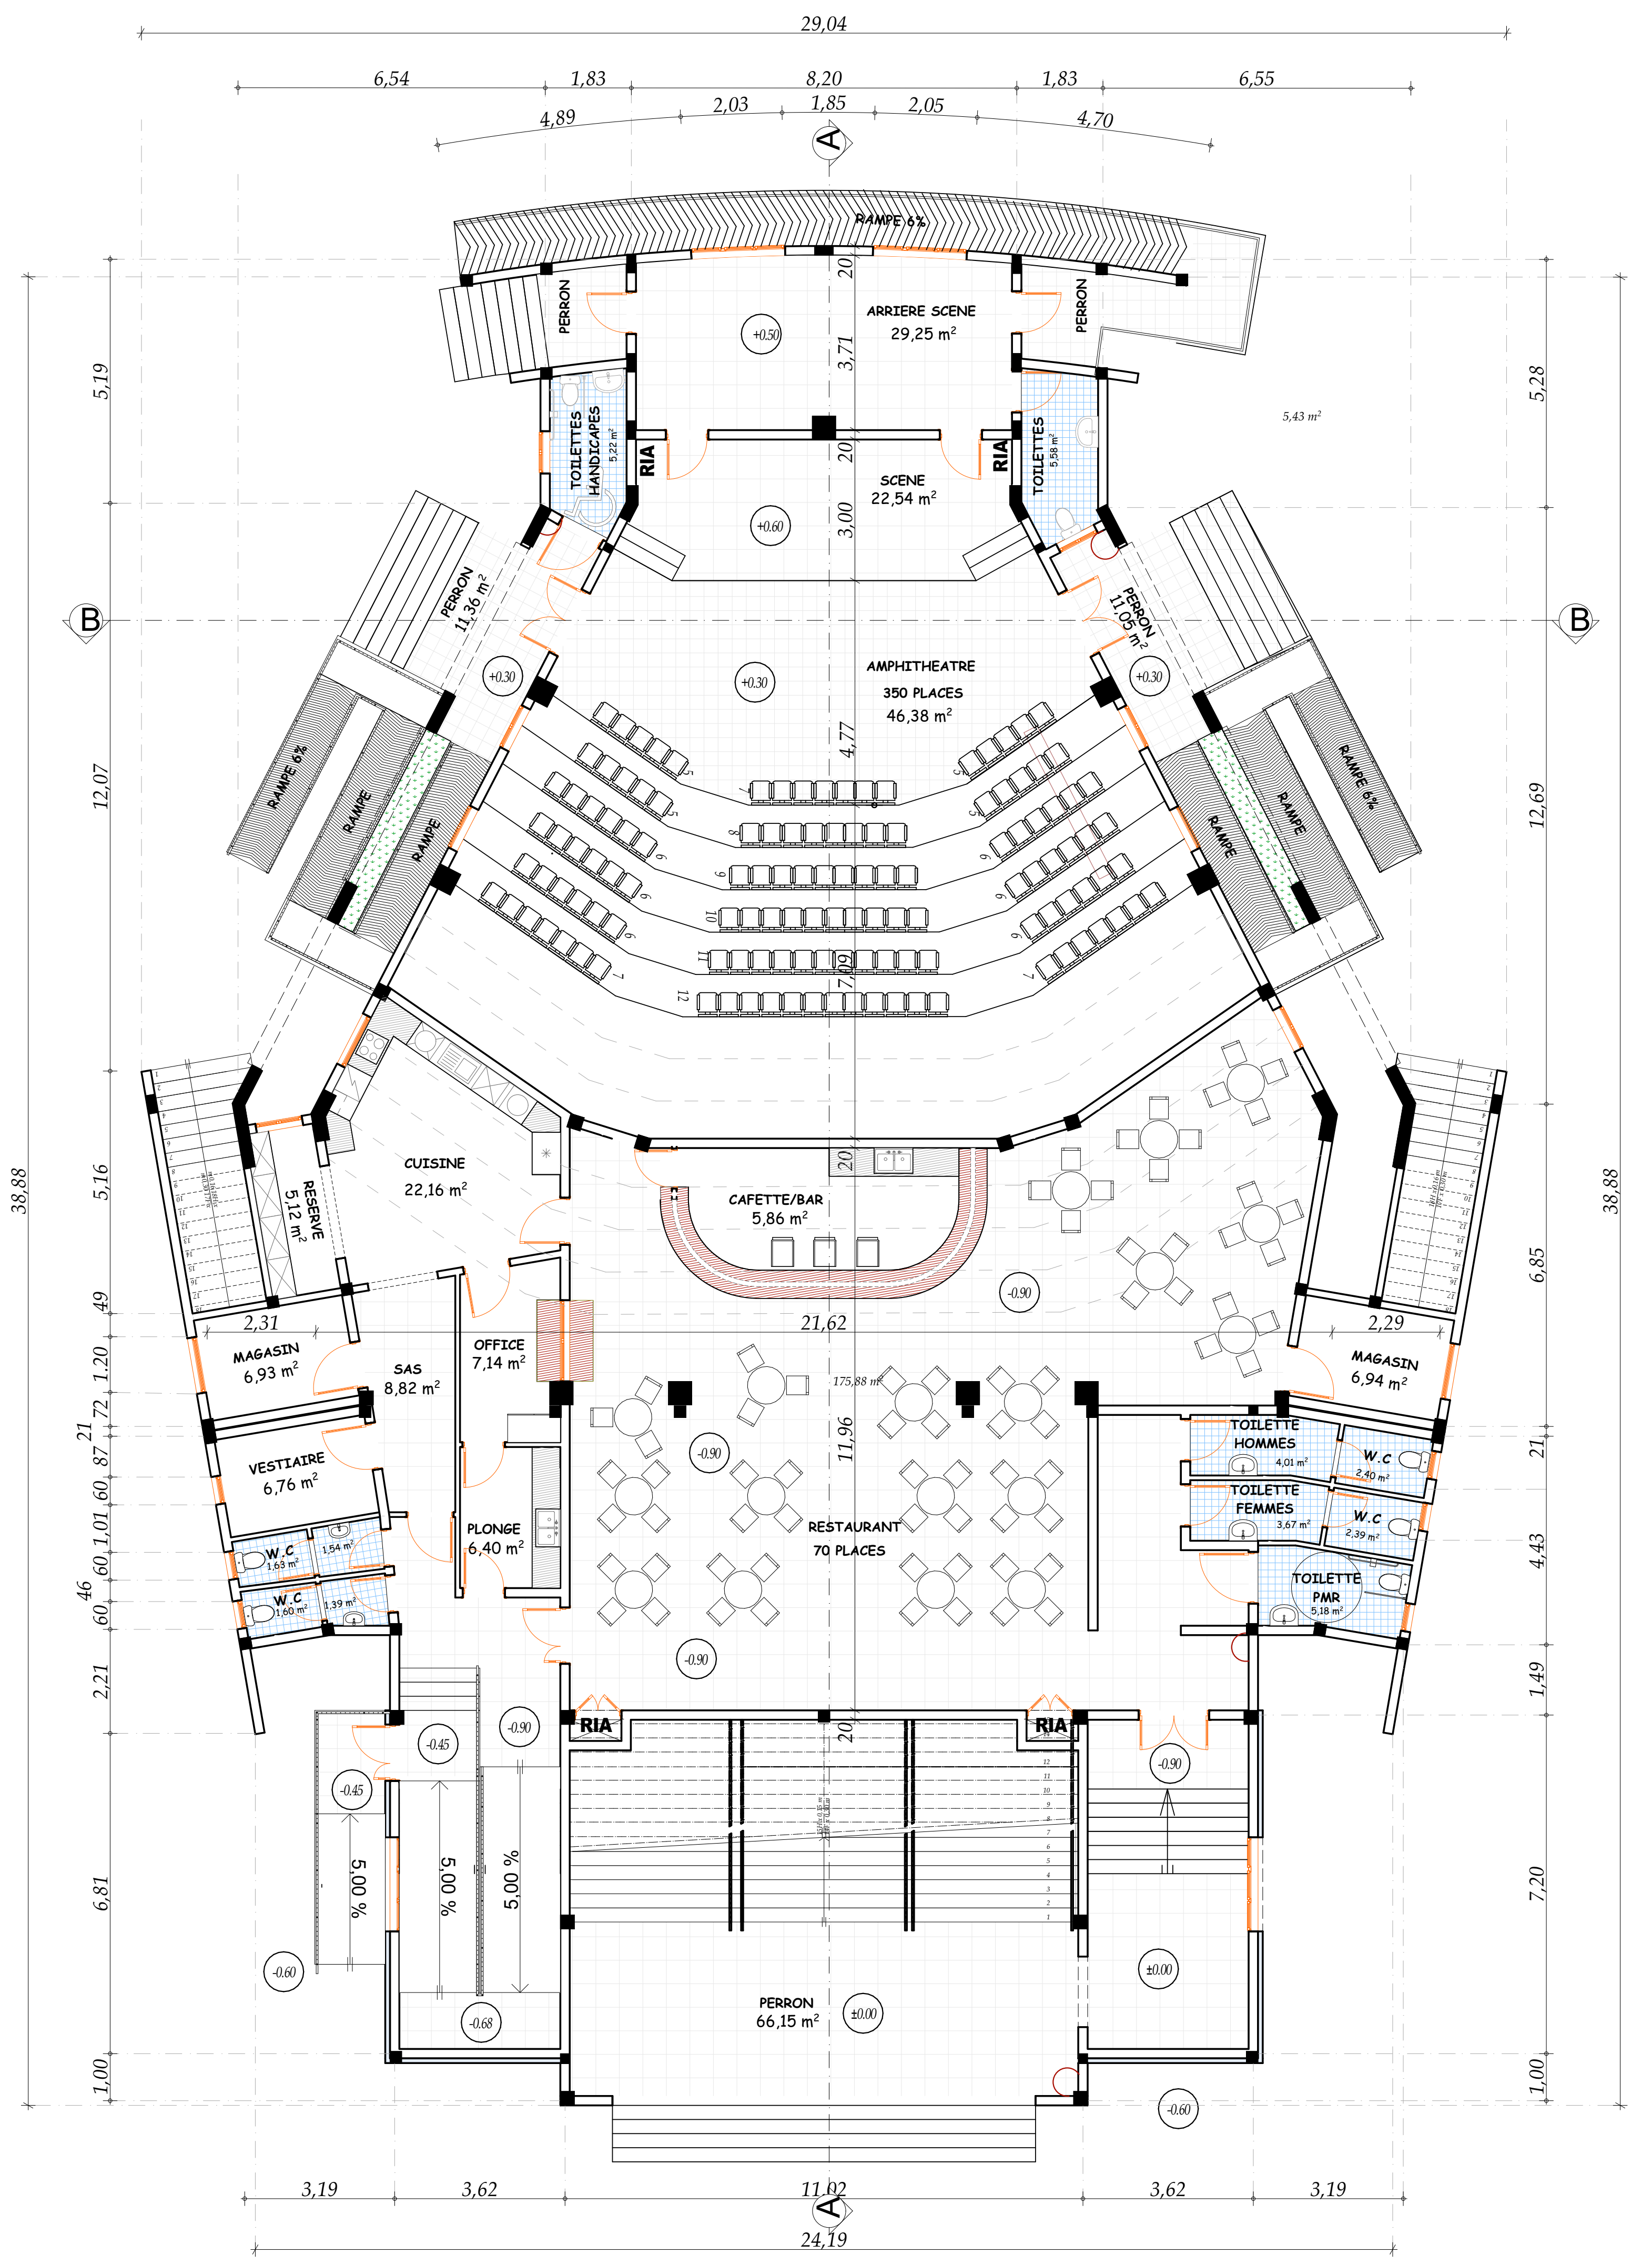

29,04
6,54
1,83
8,20
1,83
6,55
4,89
2,03
1,85
2,05
4,70
A
RAMPE 6%
PERRON
ARRIERE SCENE
29,25 m²
TOILETTES HANDICAPES
RIA
SCENE
22,54 m²
TOILETTES
B
AMPHITHEATRE
350 PLACES
46,38 m²
RAMPE 6%
RAMPE
CUISINE
22,16 m²
RESERVE
CAFETTE/BAR
5,86 m²
21,62
MAGASIN
6,93 m²
SAS
8,82 m²
OFFICE
7,14 m²
MAGASIN
6,94 m²
VESTIAIRE
6,76 m²
PLONGE
6,40 m²
RESTAURANT
70 PLACES
TOILETTE HOMMES
TOILETTE FEMMES
TOILETTE PMR
W.C
5,00 %
PERRON
66,15 m²
3,19
3,62
11,02
3,62
3,19
24,19
38,88

PLAN DE NIVEAU RDC

ECHELLE 1/100

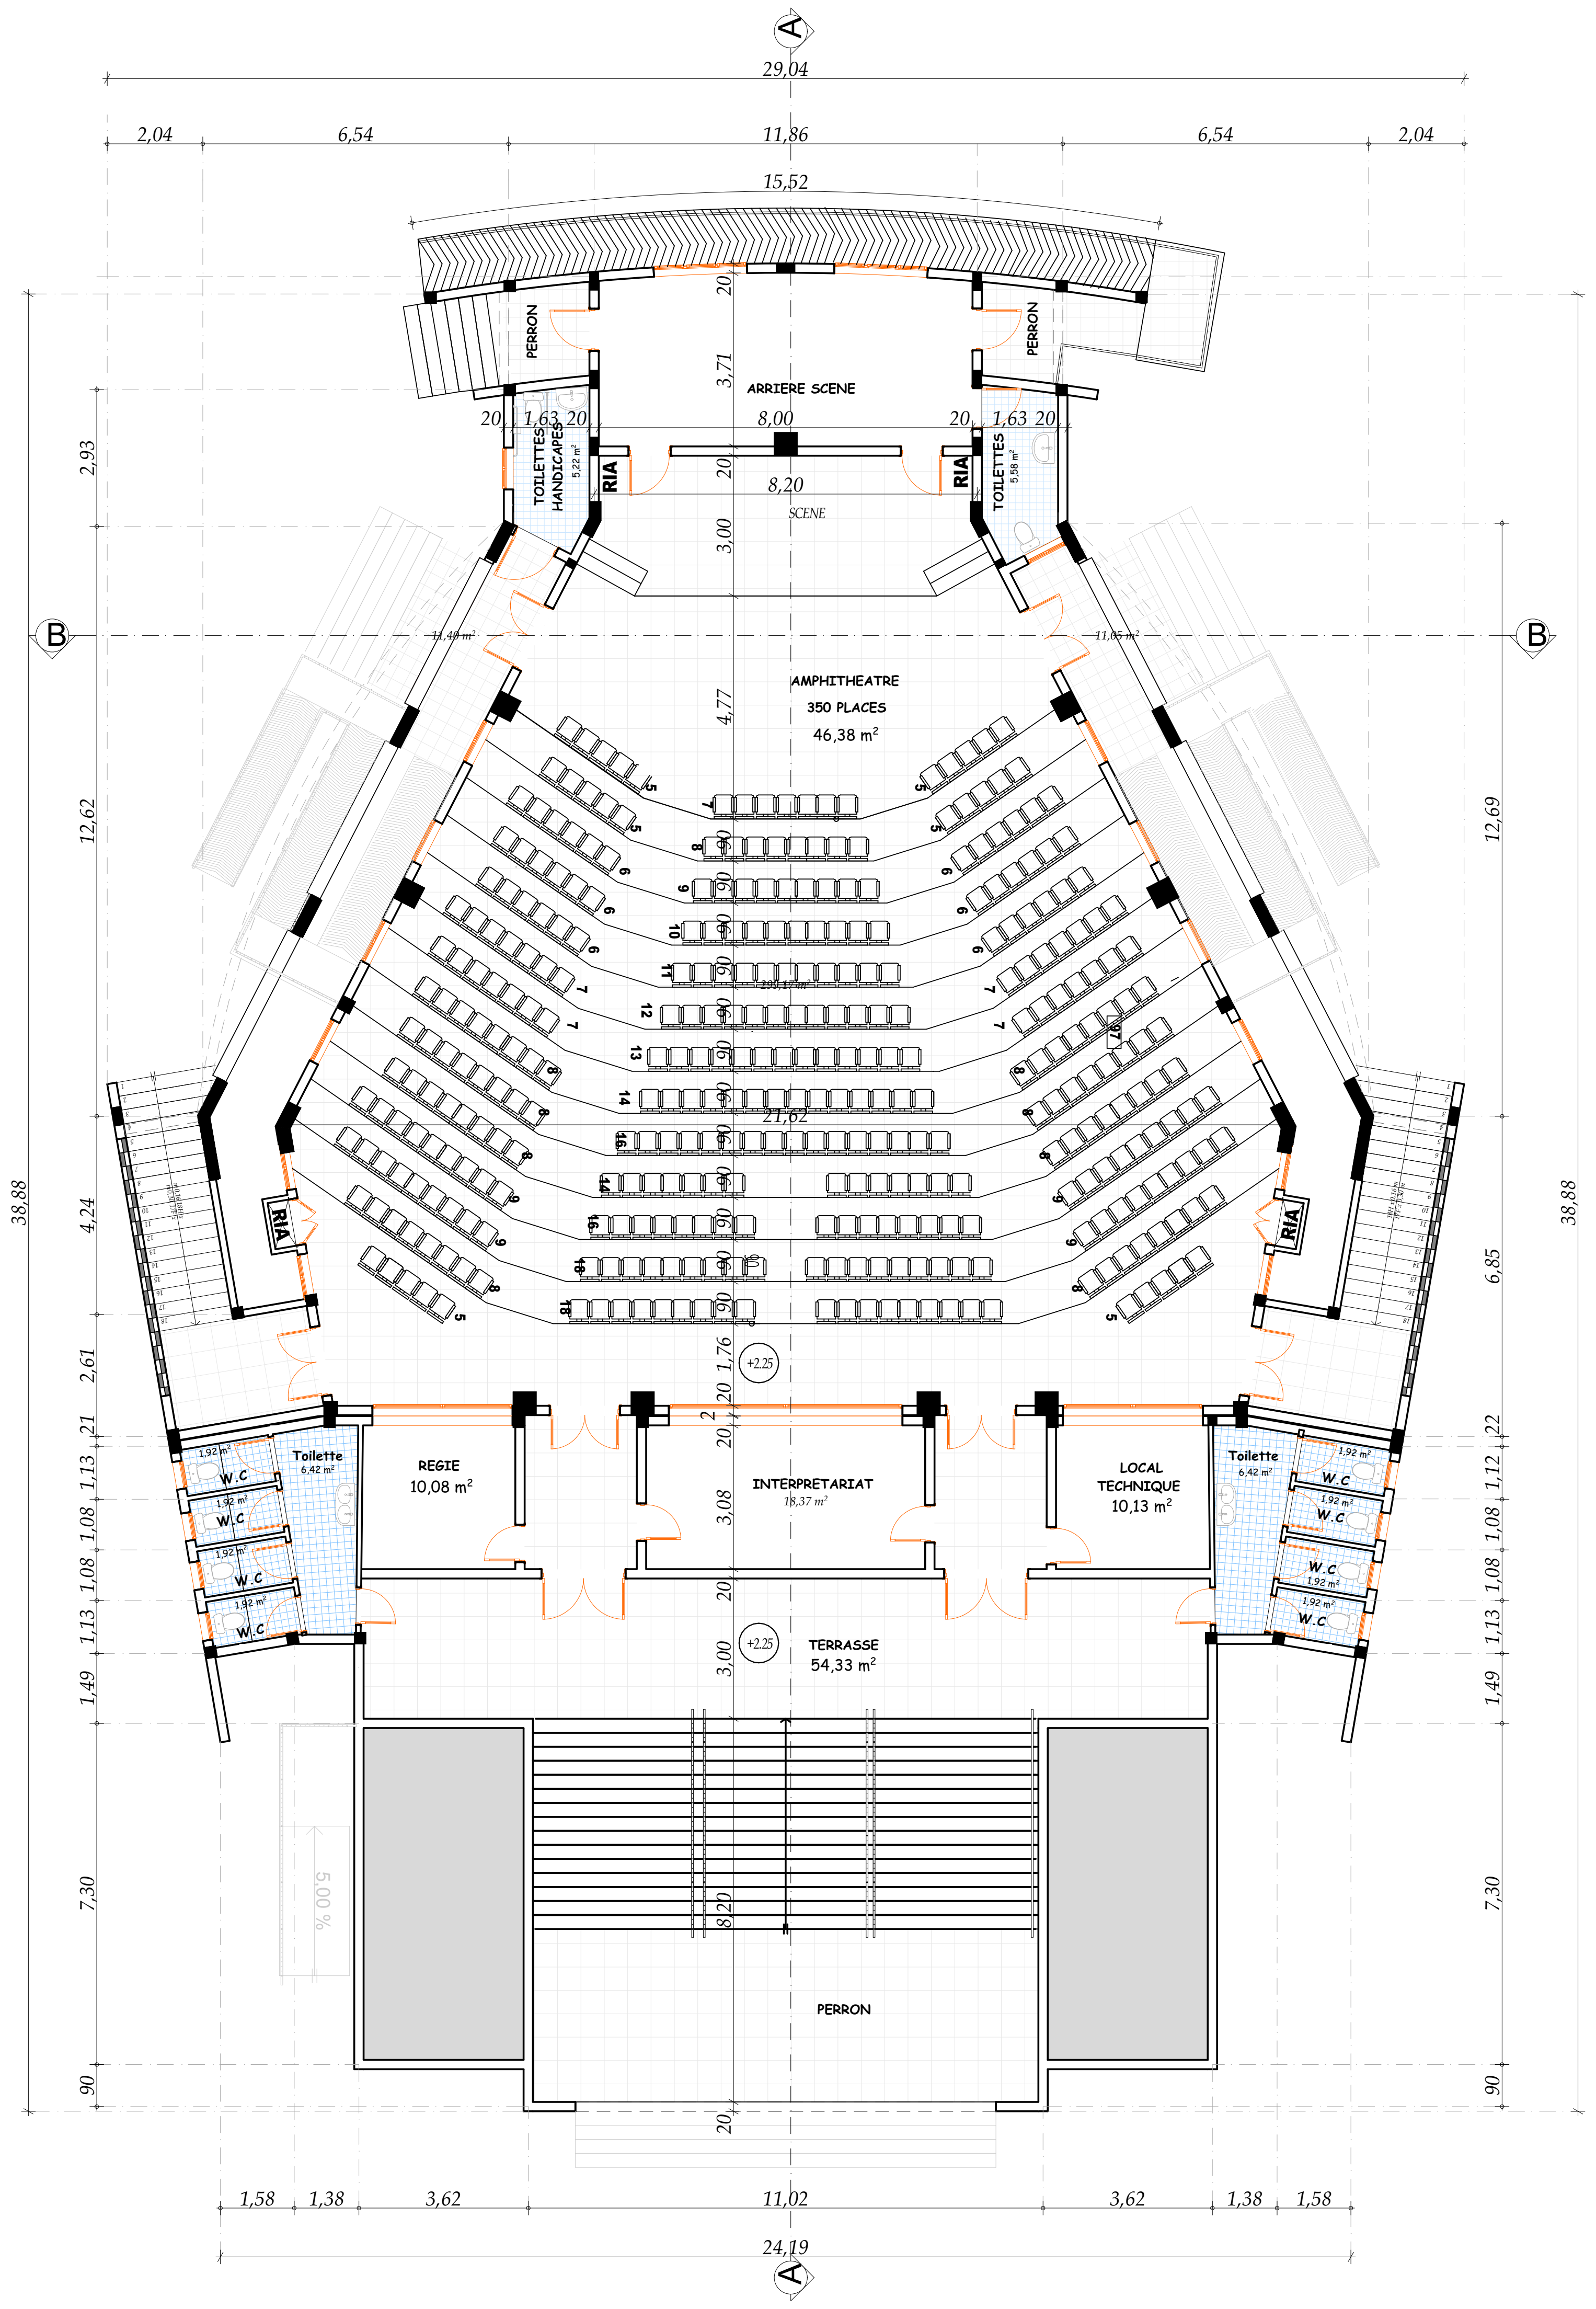

A
29,04
2,04
6,54
11,86
6,54
2,04
15,52
ARRIERE SCENE
8,00
8,20
SCENE
TOILETTES HANDICAPES
RIA
B
AMPHITHEATRE
350 PLACES
46,38 m²
RIA
REGIE
10,08 m²
INTERPRETARIAT
LOCAL TECHNIQUE
10,13 m²
Toilette
W.C
TERRASSE
54,33 m²
PERRON
1,58
1,38
3,62
11,02
3,62
1,38
1,58
24,19
38,88

PLAN DE NIVEAU MEZZANINE (A hauteur de 3.25 m)de ±0.00

ECHELLE 1/100

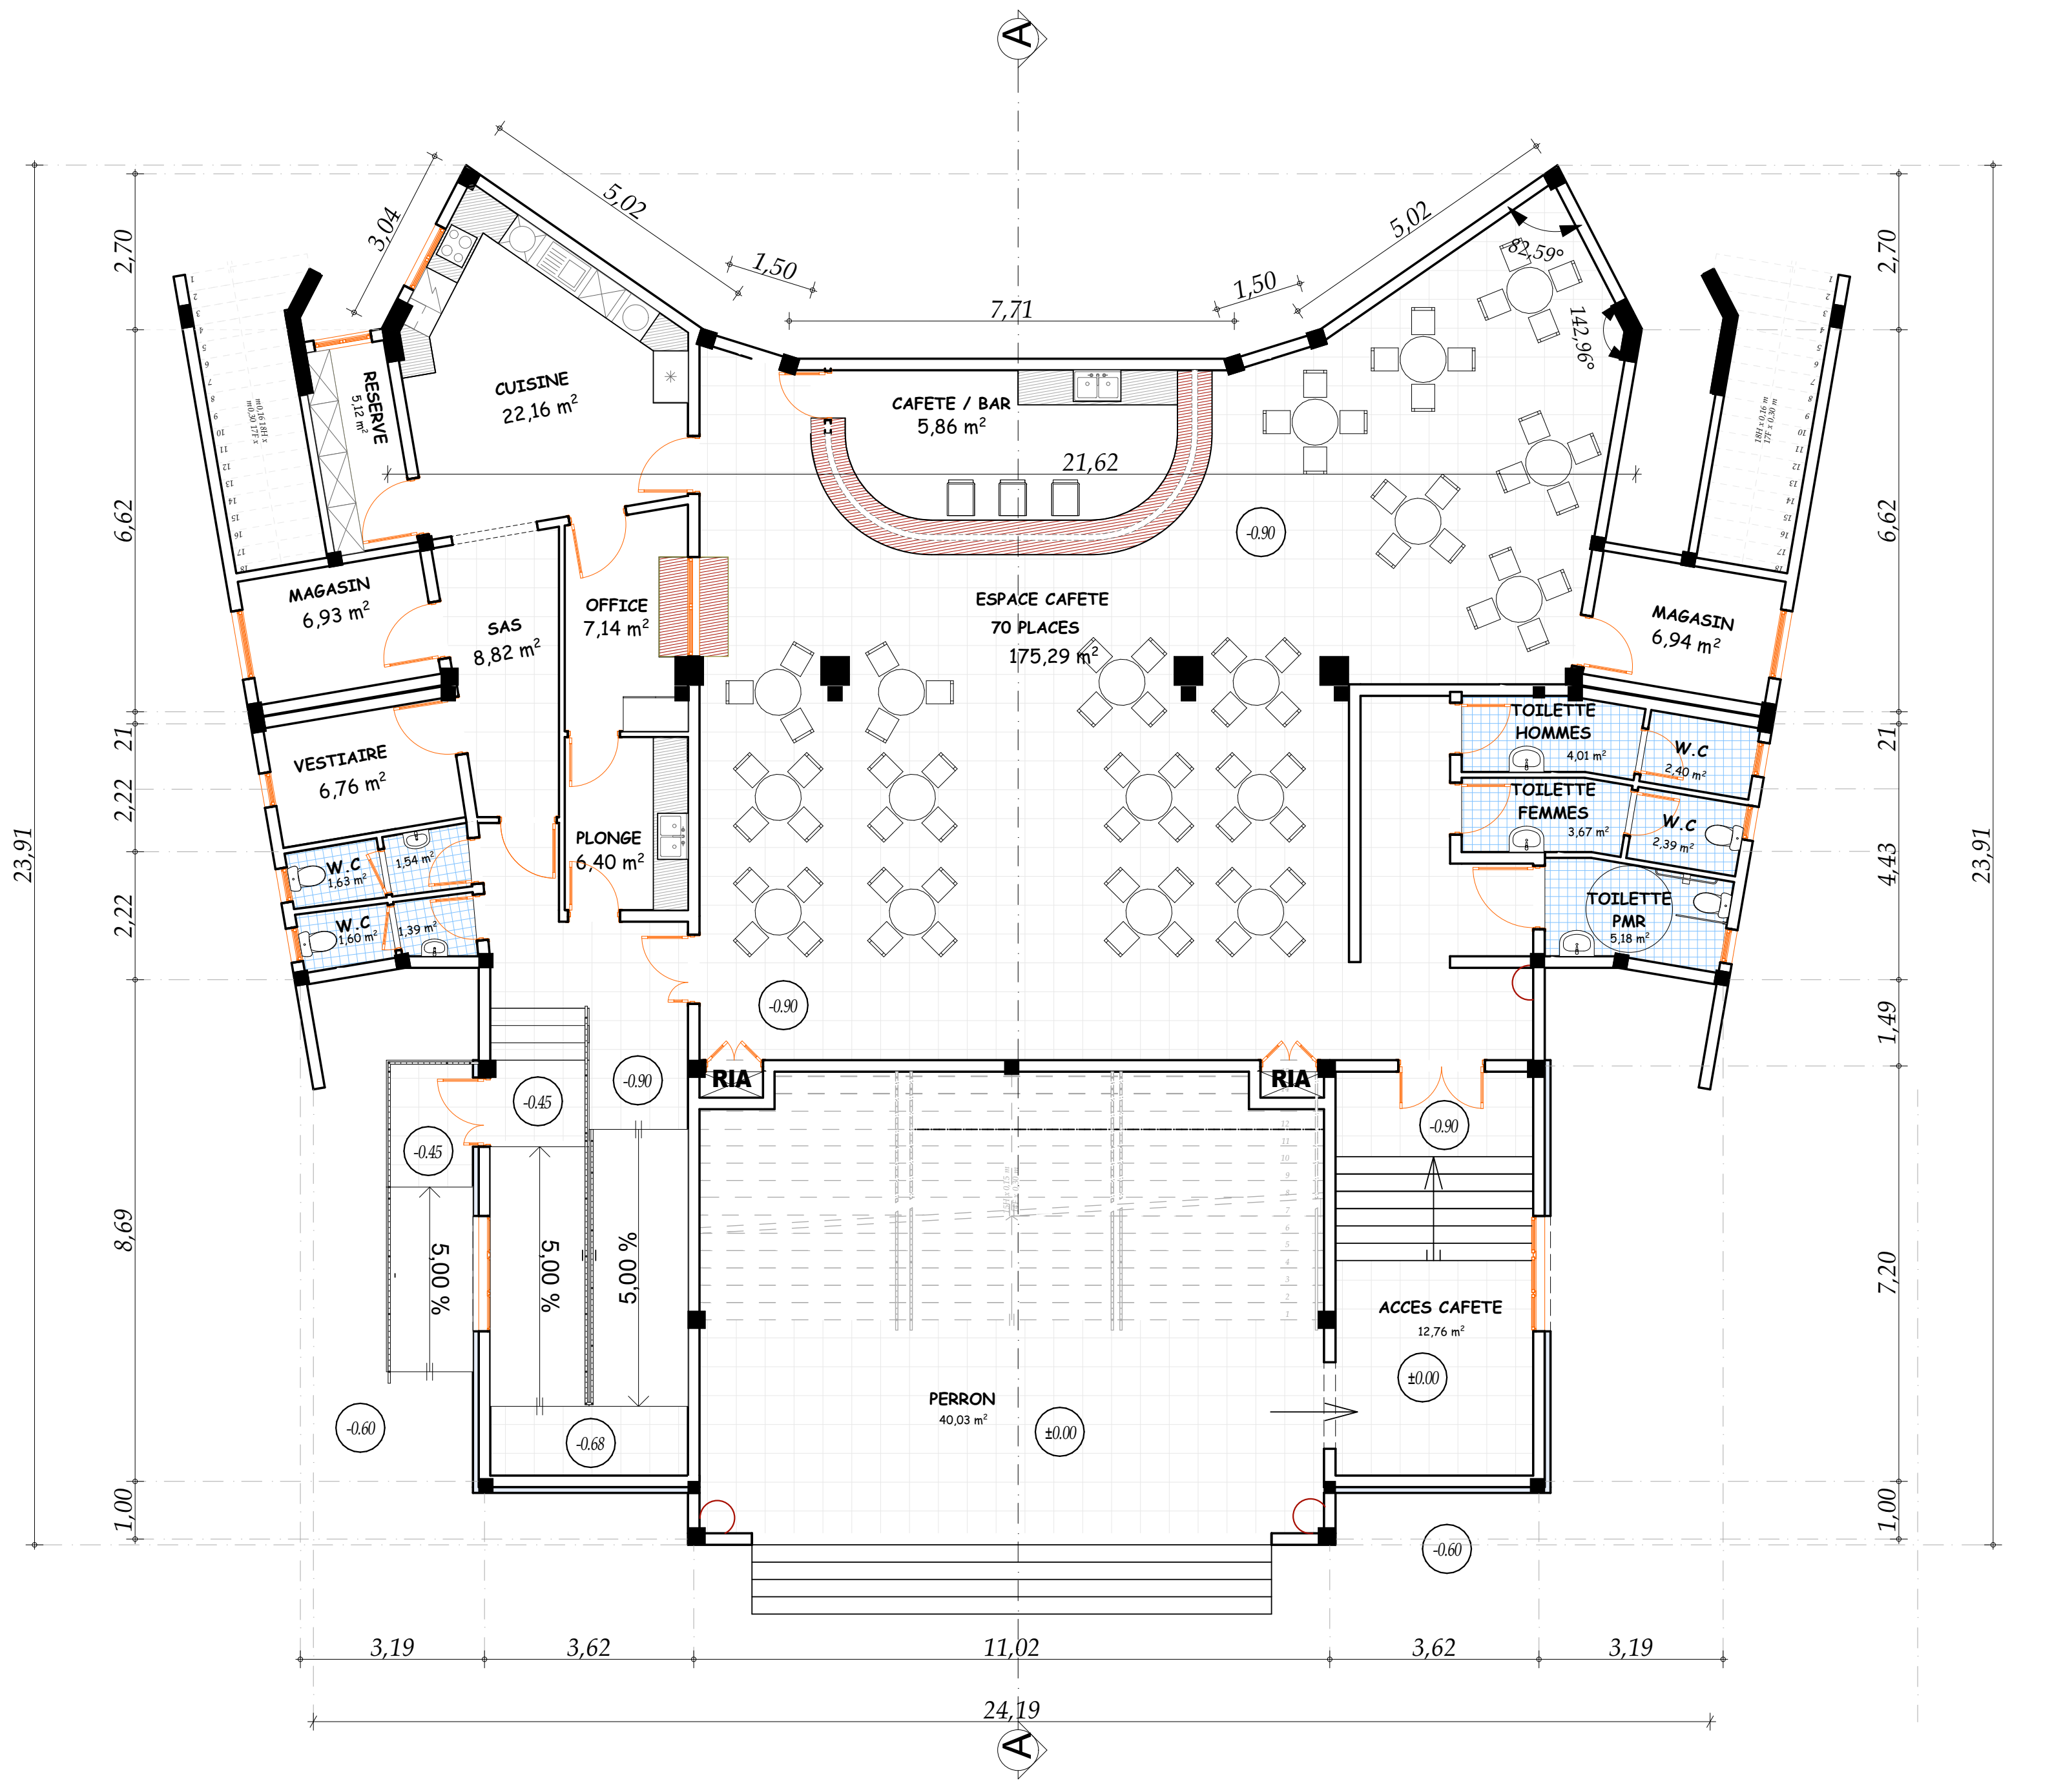

A
5,02
1,50
7,71
1,50
5,02
CUISINE
22,16 m²
RESERVE
CAFETE / BAR
5,86 m²
21,62
MAGASIN
6,93 m²
SAS
8,82 m²
OFFICE
7,14 m²
ESPACE CAFETE
70 PLACES
175,29 m²
MAGASIN
6,94 m²
VESTIAIRE
6,76 m²
PLONGE
6,40 m²
TOILETTE HOMMES
TOILETTE FEMMES
TOILETTE PMR
W.C
RIA
5,00 %
PERRON
ACCES CAFETE
3,19
3,62
11,02
3,62
3,19
24,19
23,91

PLAN DE NIVEAU RDC CAFETE

ECHELLE 1/100

BURKINA FASO
Unité-Progres-Justice

PROJET DE CONSTRUCTION ET D'EQUIPEMENT D'UNE UNITE DE FORMATION ET DE RECHERCHE EN SCIENCES ET TECHNIQUES (UFR/ST) ET D'UNE CITE UNIVERSITAIRE AU CENTRE UNIVERSITAIRE POLYTECHNIQUE DE DORI ET D'UNE CITE UNIVERSITAIRE A L'UNIVERSITE DE FADA N'GOURMA

Maître d'ouvrage délégué	Maître d'ouvrage	Financement
DIRECTION DES PROJETS CITES UNIVERSITAIRES (DPCU)	MINISTERE DE L'ENSEIGNEMENT SUPERIEUR, DE LA RECHERCHE SCIENTIFIQUE ET DE L'INNOVATION (MESRSI)	BADEA/OFID

MAÎTRE D'OEUVRE : GROUPEMENT

CINCAT INTERNATIONAL S.A
Compagnie pour l'Ingénierie, la Coordination et l'Assistance Technique
01 BP : 4524 Ouagadougou 01 Burkina Faso
TEL : (226) 50 34 31 24 / 50 34 27 19 FAX : (226) 50 34 31 26
E-mail : cincat @fasonet..bf

Etudes - Recherches - Conseils - Réalisations en Architecture et Ingénierie - Expertise Immobilière
ARCHITECTES - INGENIEURS CONSEILS
01 B.P 674 Ouagadougou 01
Tel.25.31.53.52
E.mail:info@aicagencebf.com
www.aicagencebf.com

MOSAIQUE INGENIERIE
Adresse : N°16 Rue de Syrie, Imm. EPI CENTER Bloc 'C' 9ème étage BP 1002 Tunis Belvédère- Tunisie
E-mail : headoffice@mosaique-ingenierie.com
Tél : (+216) 71 889 350 - 71 831 522
Fax : (+216) 71 871 060 - 71 831 501
Site Web : www.mosaique-ingenierie.com

DOSSIER D'APPEL D'OFFRE (DAO)

Bureau de contrôle technique	LOT N°		PLANCHE N°	ECHELLE
	1.1	I.3 AMPHITHEATRE PLAN DE NIVEAU RDC,CAFETE ET MEZZANINE	ASA 01	1/100
			INDICE	DATE
			00	Février 2022

DATE	MODIFICATIONS	EFFECTUEE PAR	APPROUVEE PAR

LOT 1.1:I.3 AMPHITHEATRE DE 350 PLACES (SALLE DES ACTES)

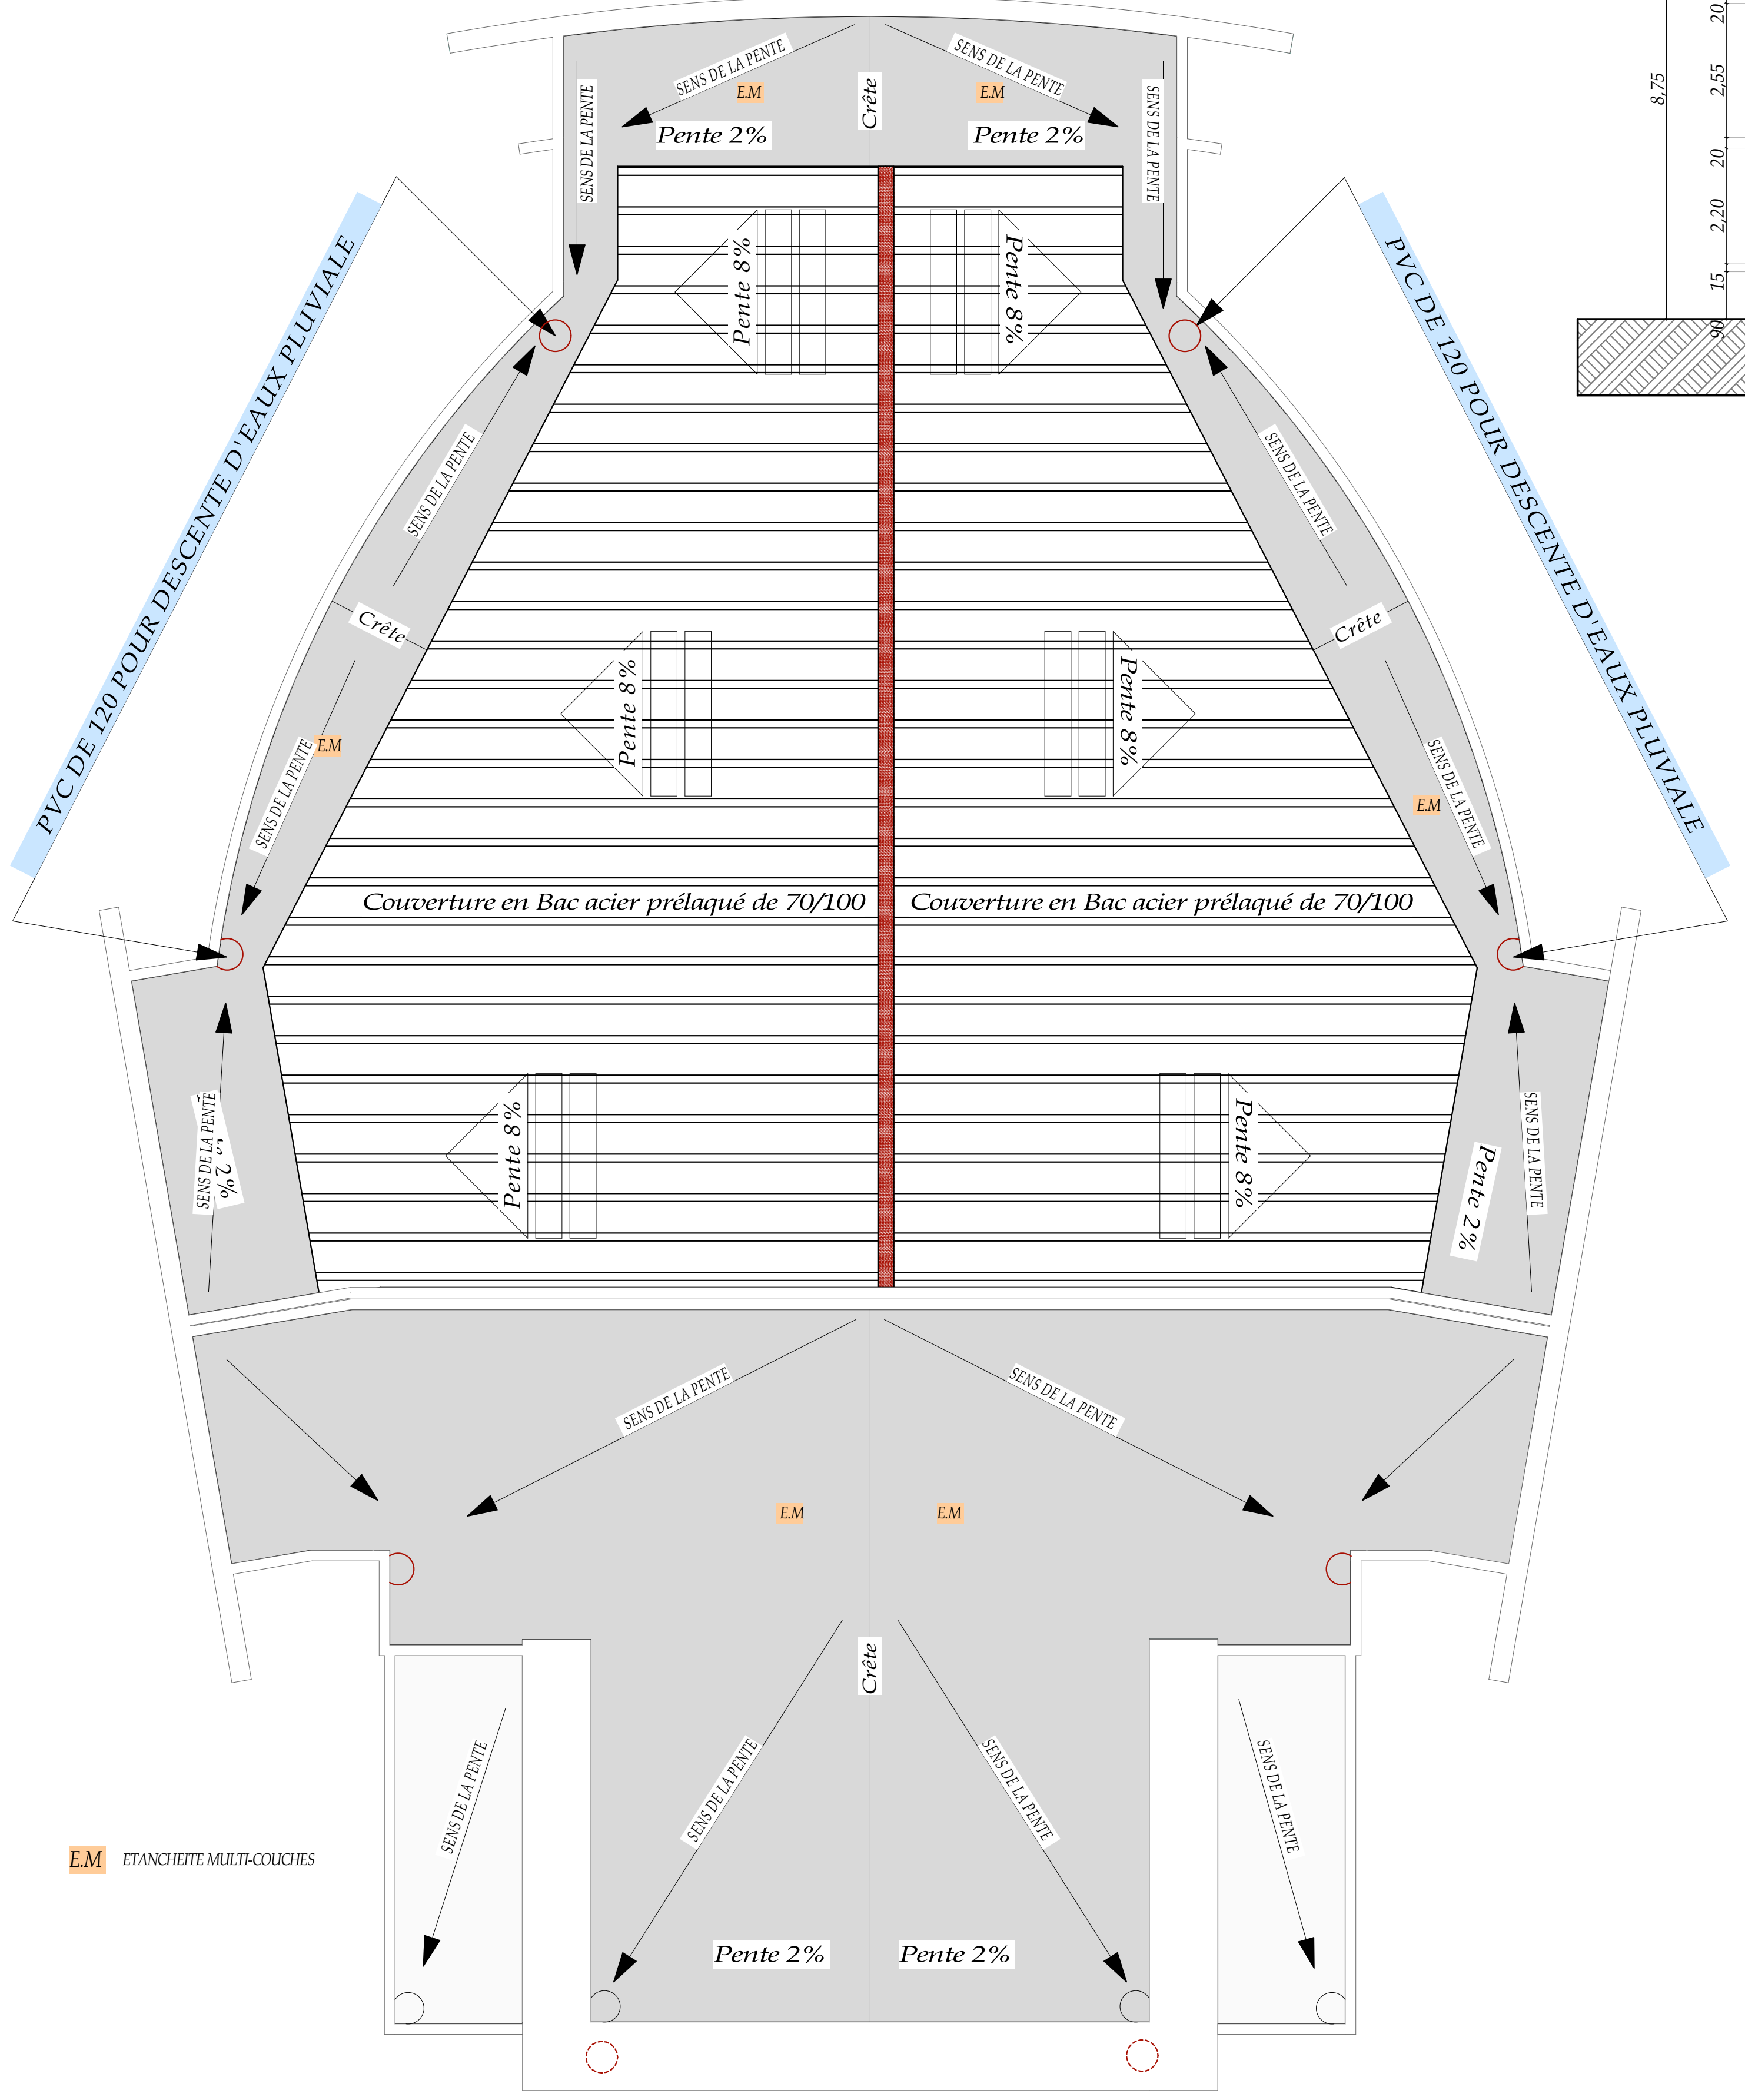
PVC DE 120 POUR DESCENTE D'EAUX PLUVIALE
PVC DE 120 POUR DESCENTE D'EAUX PLUVIALE
SENS DE LA PENTE
Crête
E.M
Pente 2%
Pente 8%
Couverture en Bac acier prélaqué de 70/100
Couverture en Bac acier prélaqué de 70/100
E.M ETANCHEITE MULTI-COUCHES

PLAN DE TOITURE

ECHELLE 1/100

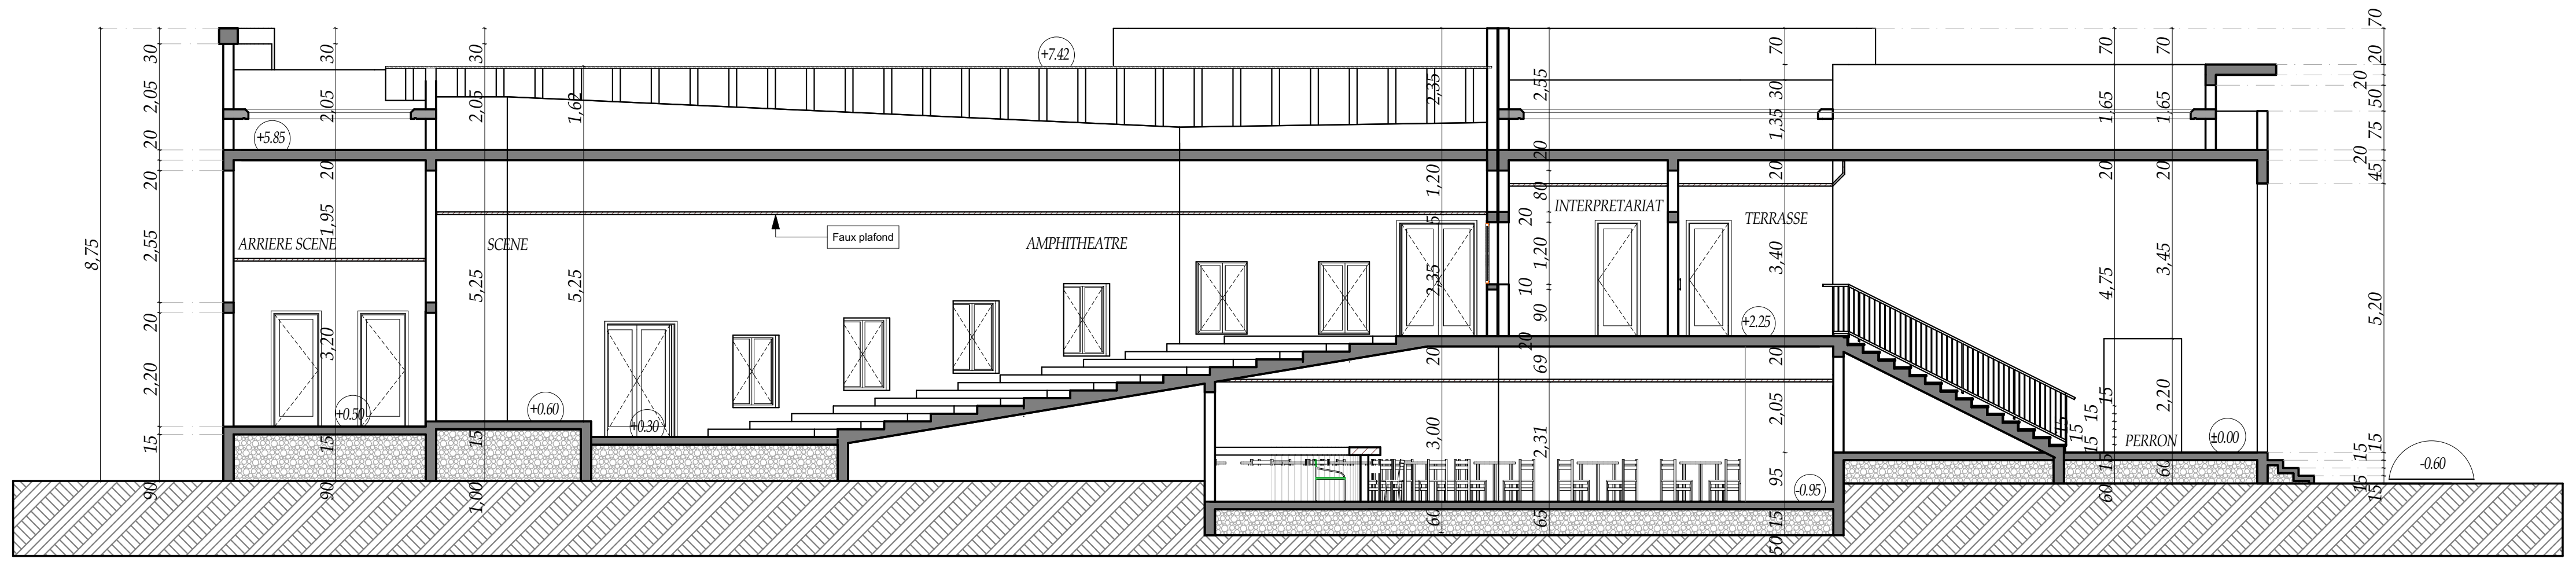
ARRIERE SCENE
SCENE
Faux plafond
AMPHITHEATRE
INTERPRETARIAT
TERRASSE
PERRON

COUPE A-A

ECHELLE 1/100

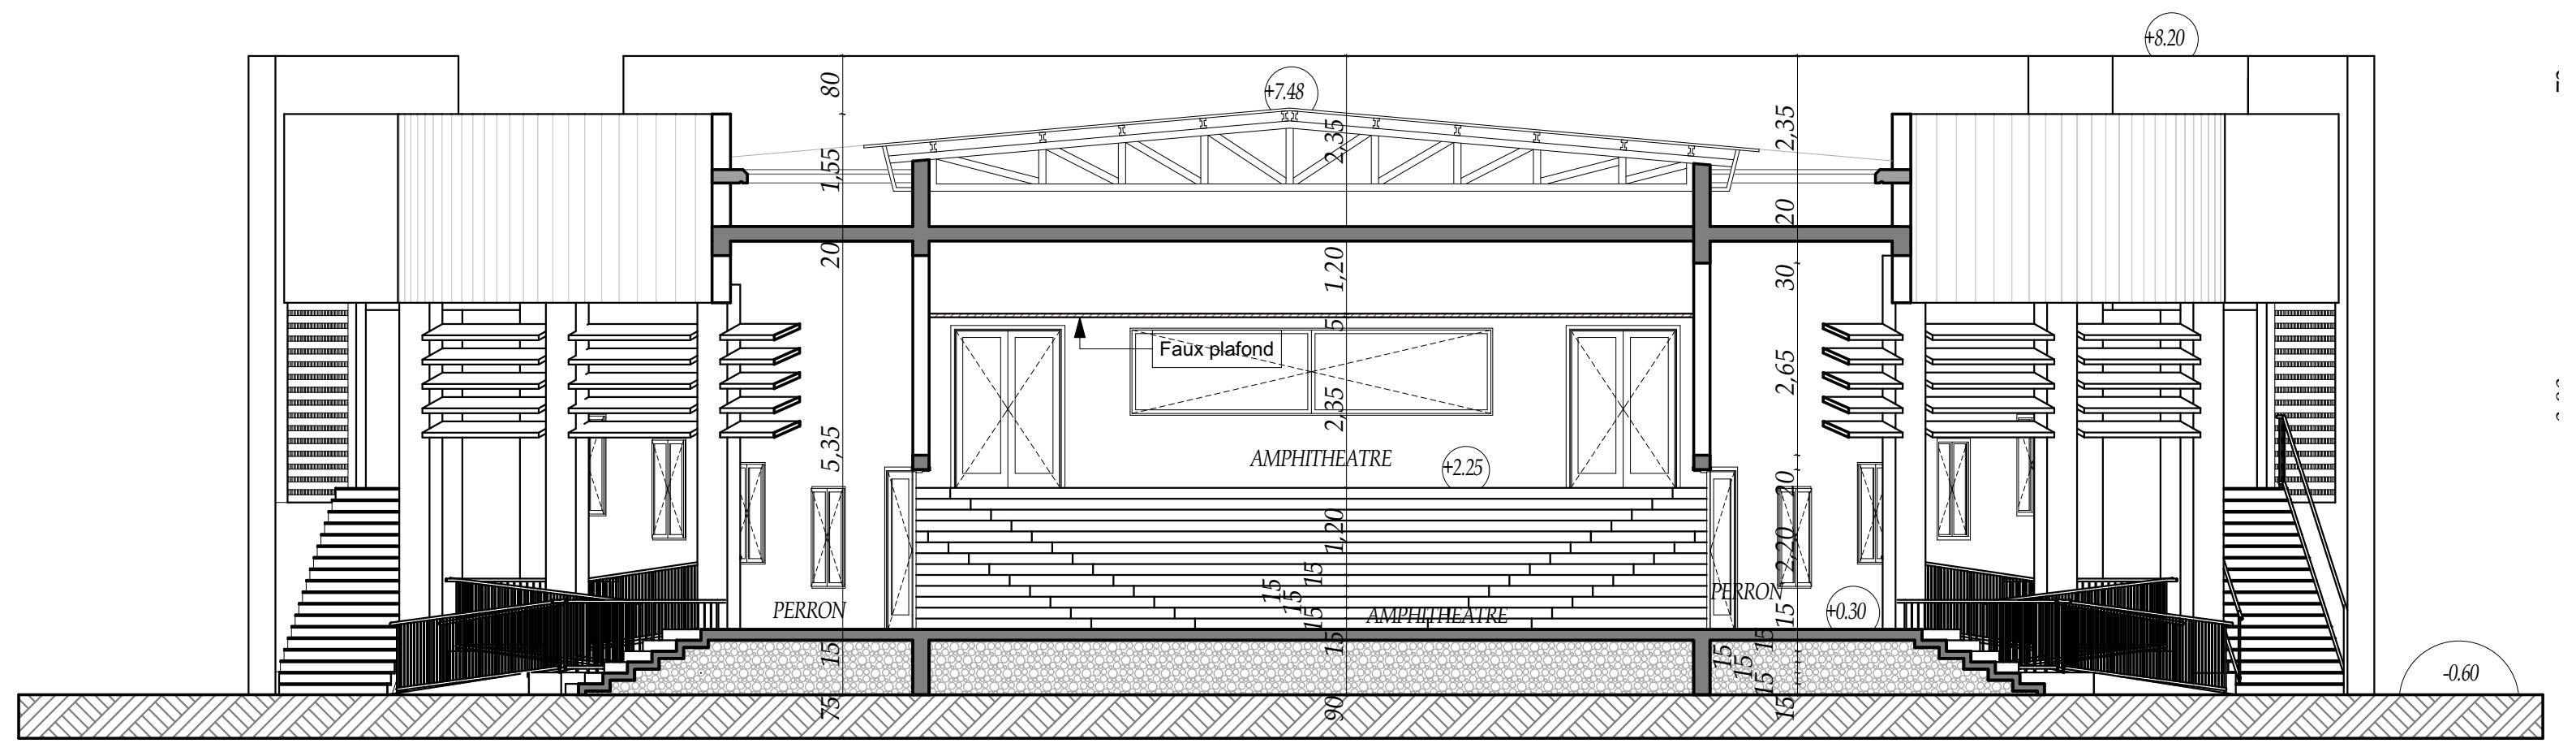
Faux plafond
AMPHITHEATRE
PERRON
PERRON

COUPE B-B

ECHELLE 1/100

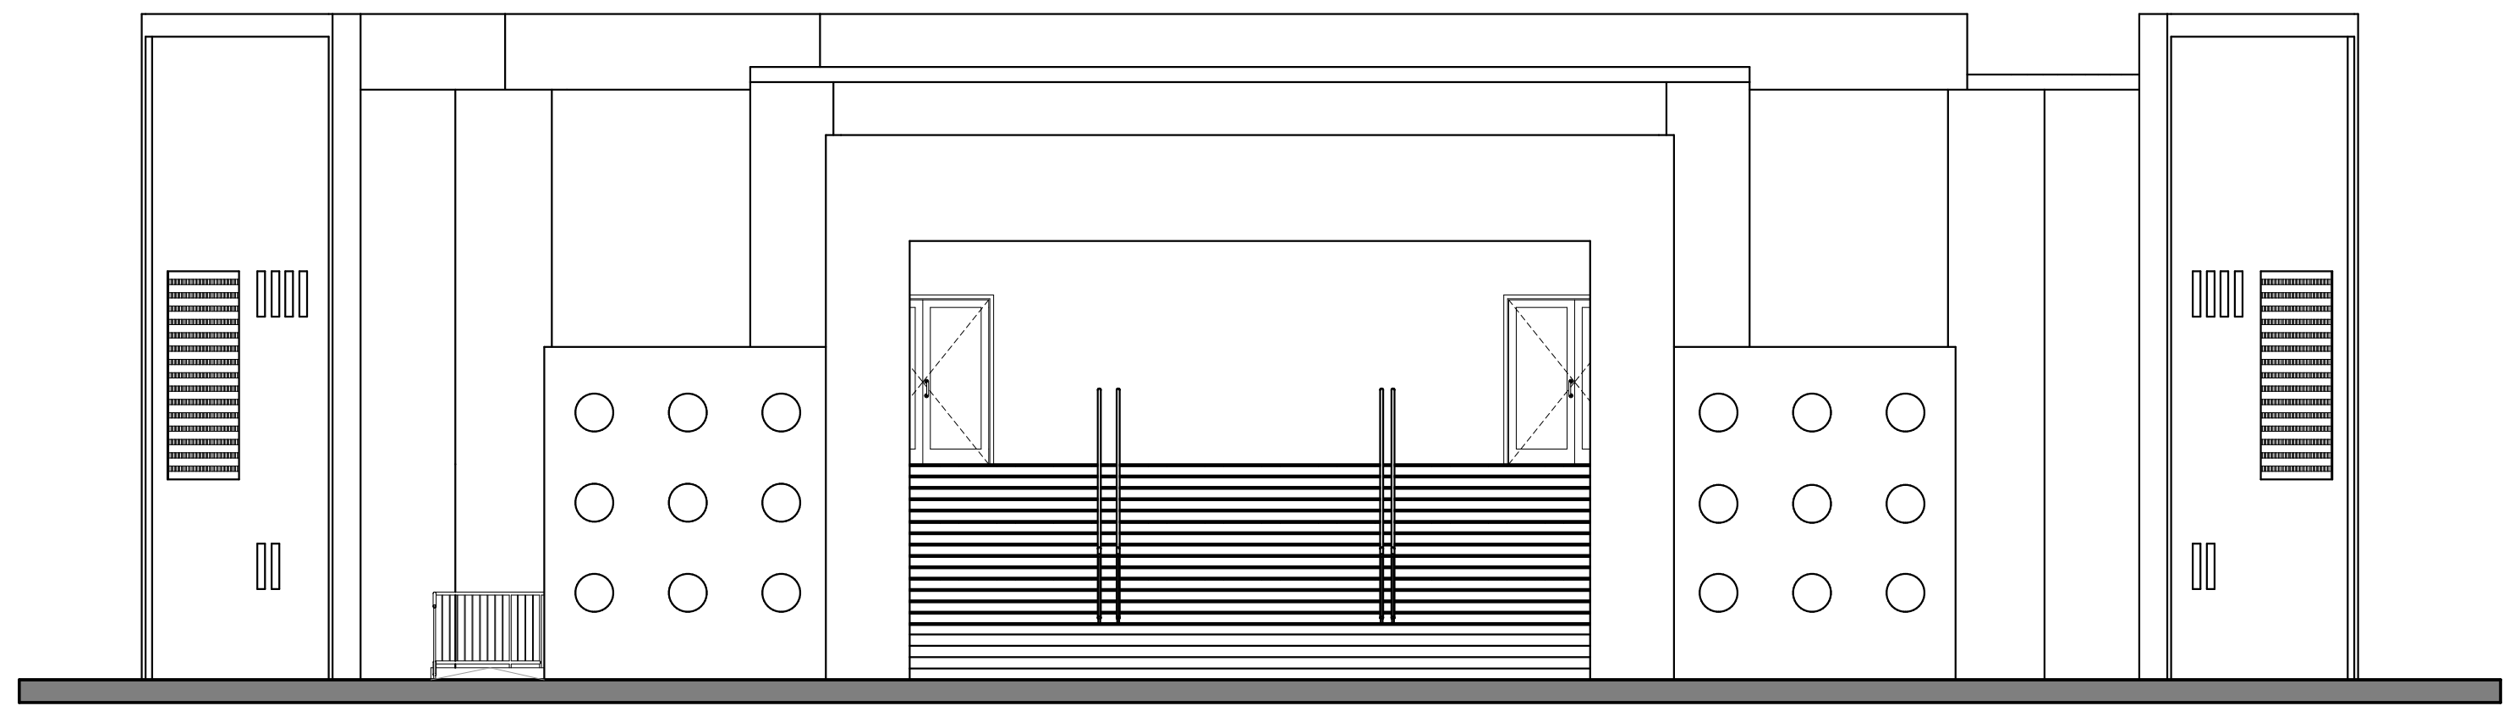

FACADE PRINCIPALE

ECHELLE 1/100

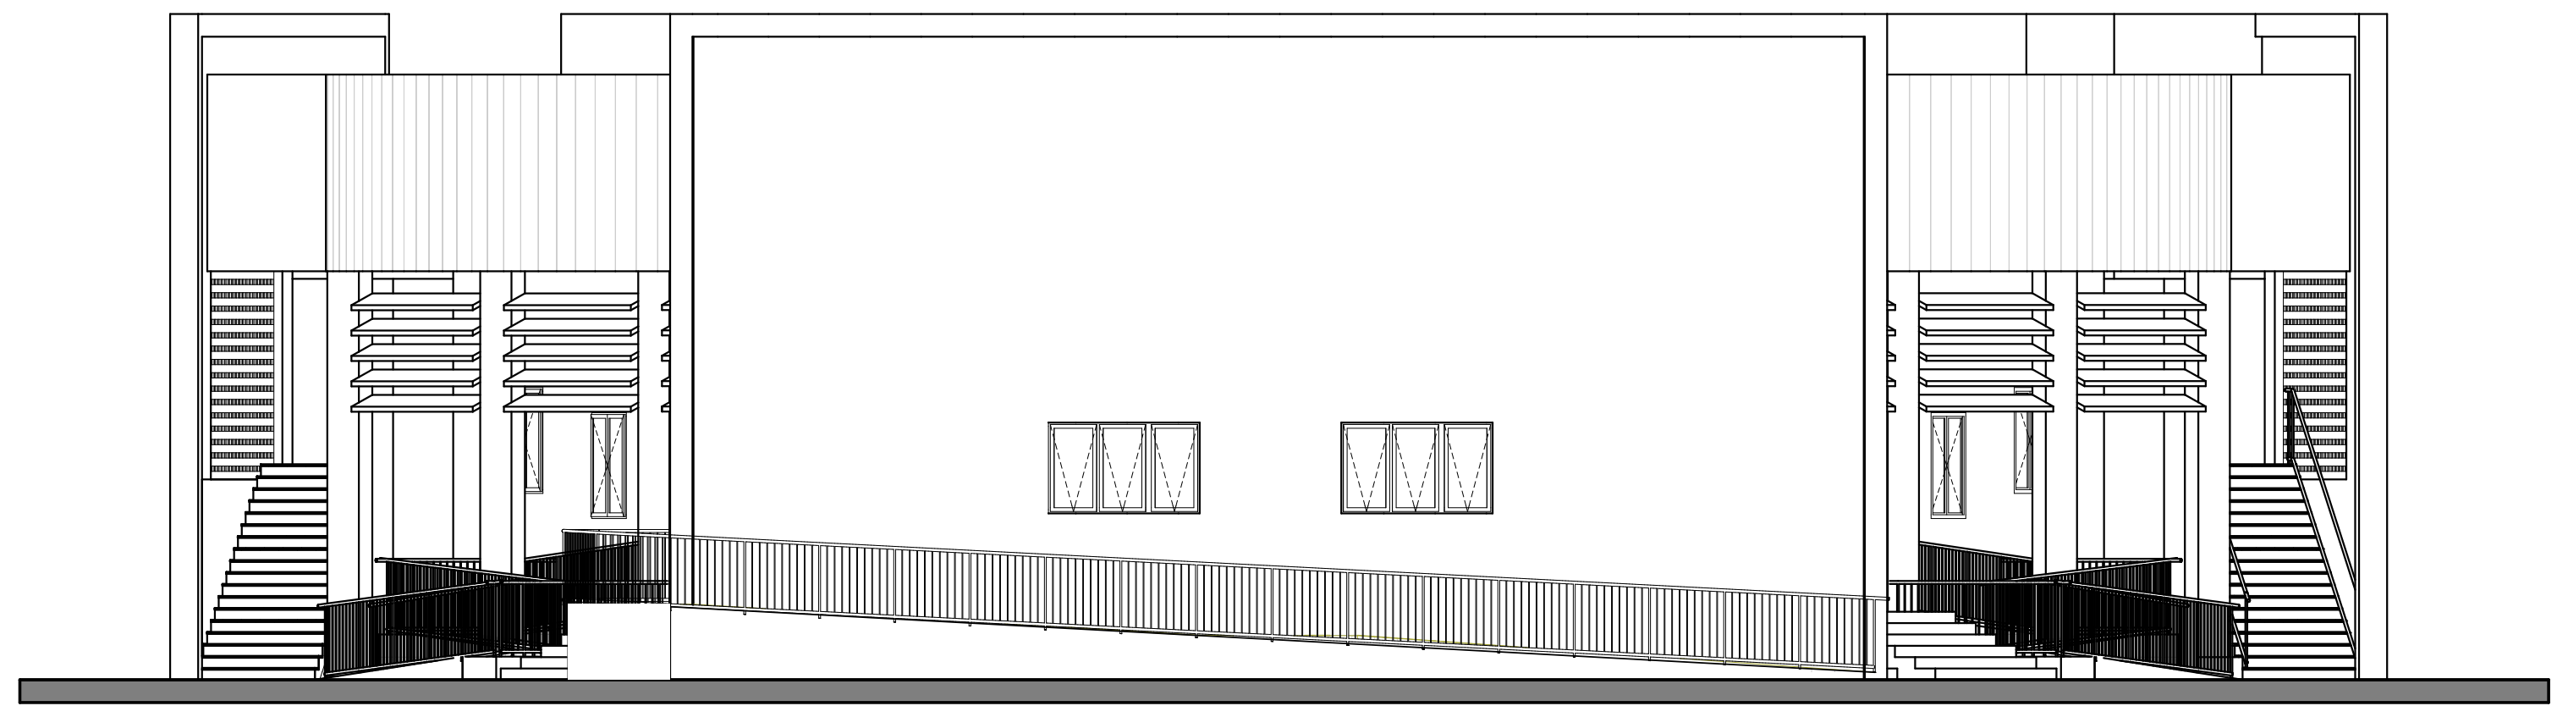

FACADE POSTERIEURE

ECHELLE 1/100

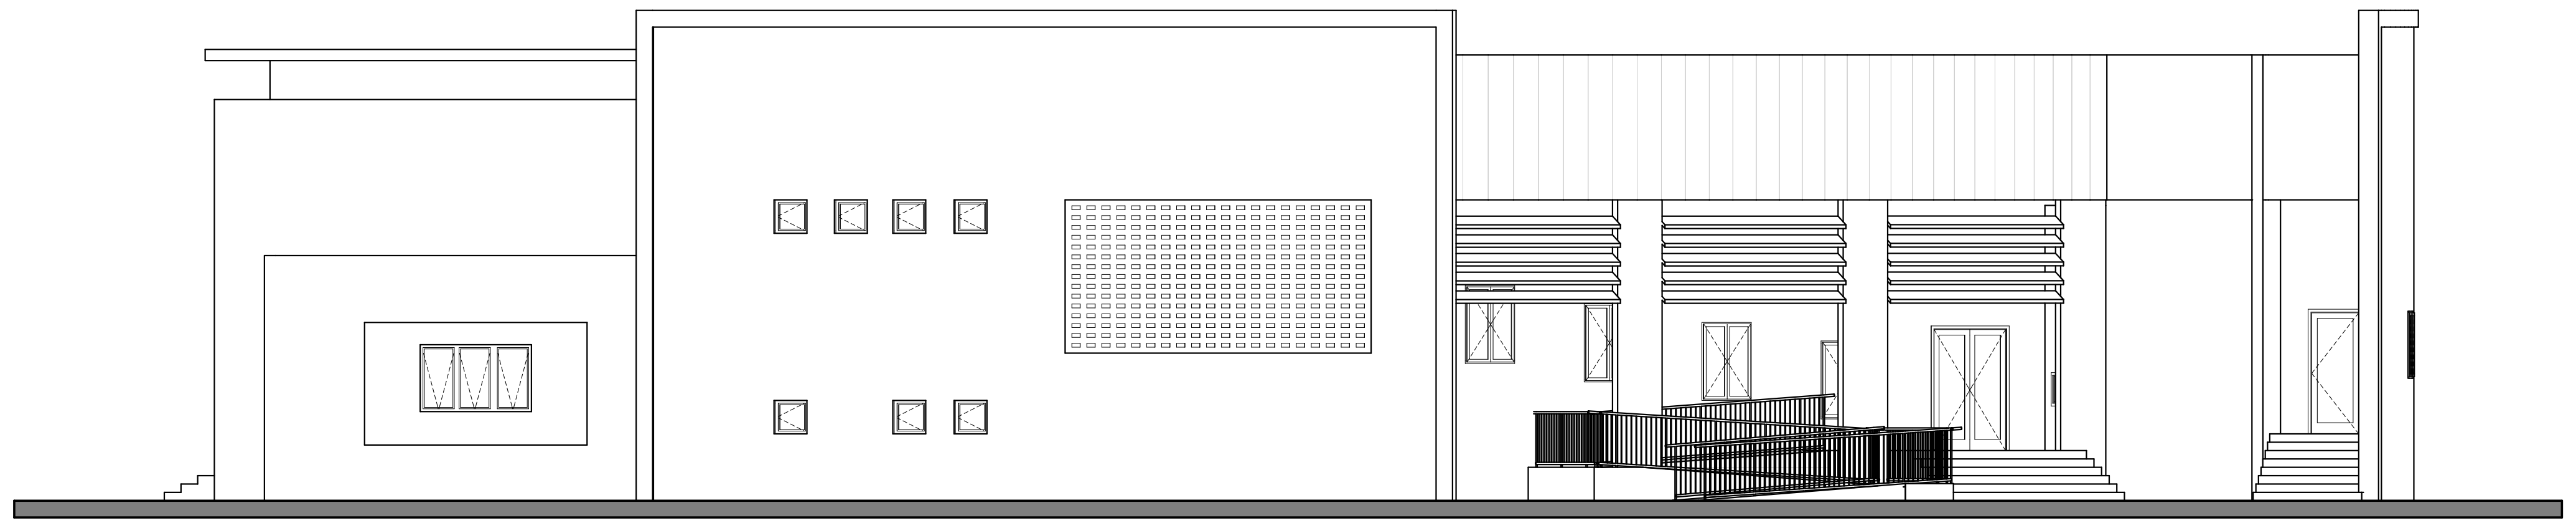

FACADE LATERALE DROITE

ECHELLE 1/100

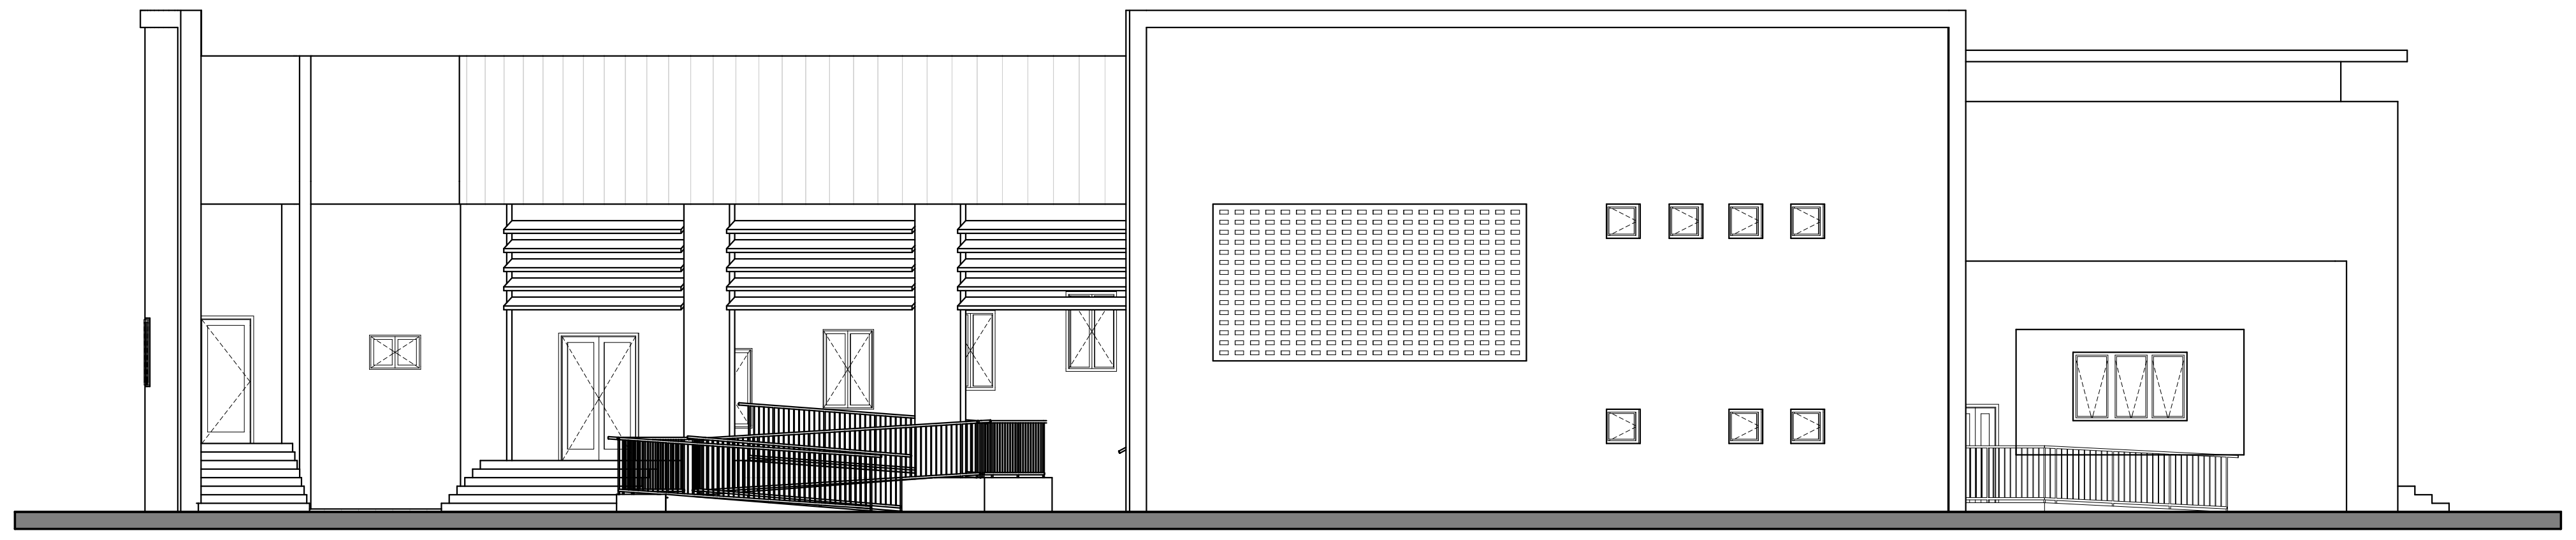

FACADE LATERALE GAUCHE

ECHELLE 1/100

BURKINA FASO
Unité-Progres-Justice

PROJET DE CONSTRUCTION ET D'EQUIPEMENT D'UNE UNITE DE FORMATION ET DE RECHERCHE EN SCIENCES ET TECHNIQUES (UFR/ST) ET D'UNE CITE UNIVERSITAIRE AU CENTRE UNIVERSITAIRE POLYTECHNIQUE DE DORI ET D'UNE CITE UNIVERSITAIRE A L'UNIVERSITE DE FADA N'GOURMA

Maître d'ouvrage délégué	Maître d'ouvrage	Financement
DIRECTION DES PROJETS CITES UNIVERSITAIRES (DPCU)	**MINISTERE DE L'ENSEIGNEMENT SUPERIEUR, DE LA RECHERCHE SCIENTIFIQUE ET DE L'INNOVATION (MESRSI)**	**BADEA/OFID**

MAÎTRE D'OEUVRE : GROUPEMENT

CINCAT INTERNATIONAL S.A
Compagnie pour l'Ingénierie, la Coordination et l'Assistance Technique
CINCAT
01 BP : 4524 Ouagadougou 01 Burkina Faso
TEL : (226) 50 34 31 24 / 50 34 27 19 FAX : (226) 50 34 31 26
E-mail : cincat @fasonet..bf

A.I.C
Etudes - Recherches - Conseils - Réalisations en Architecture et Ingénierie - Expertise Immobilière
ARCHITECTES - INGENIEURS CONSEILS
01 B.P 674 Ouagadougou 01
Tel.25.31.53.52
E.mail:info@aicagencebf.com
www.aicagencebf.com

MOSAIQUE INGENIERIE
Adresse : N°16 Rue de Syrie, Imm. EPI CENTER Bloc 'C' 9ème étage BP 1002 Tunis Belvédère- Tunisie
E-mail : headoffice@mosaique-ingenierie.com
Tél : (+216) 71 889 350 - 71 831 522
Fax : (+216) 71 871 060 - 71 831 501
Site Web : www.mosaique-ingenierie.com

DOSSIER D'APPEL D'OFFRE (DAO)

Bureau de contrôle technique	LOT N°		PLANCHE N°	ECHELLE
	1.1	I.3 AMPHITHEATRE FACADES,TOITURE ET COUPES	ASA 02	1/100
			INDICE	DATE
			00	Février 2022

DATE	MODIFICATIONS	EFFECTUEE PAR	APPROUVEE PAR

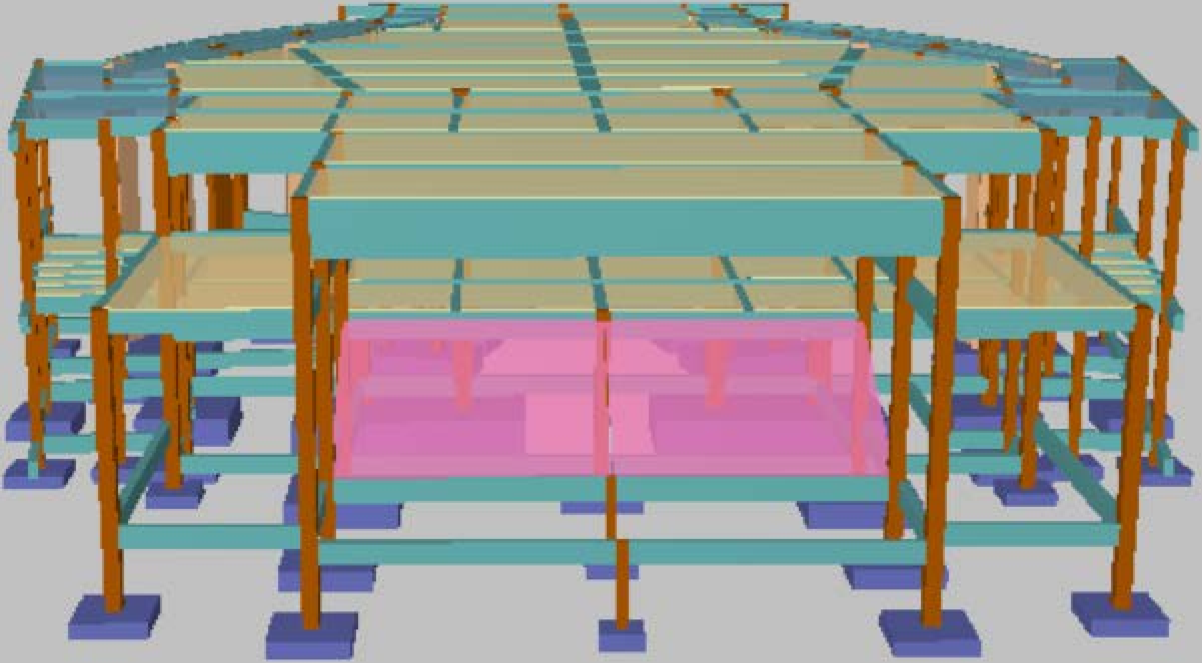

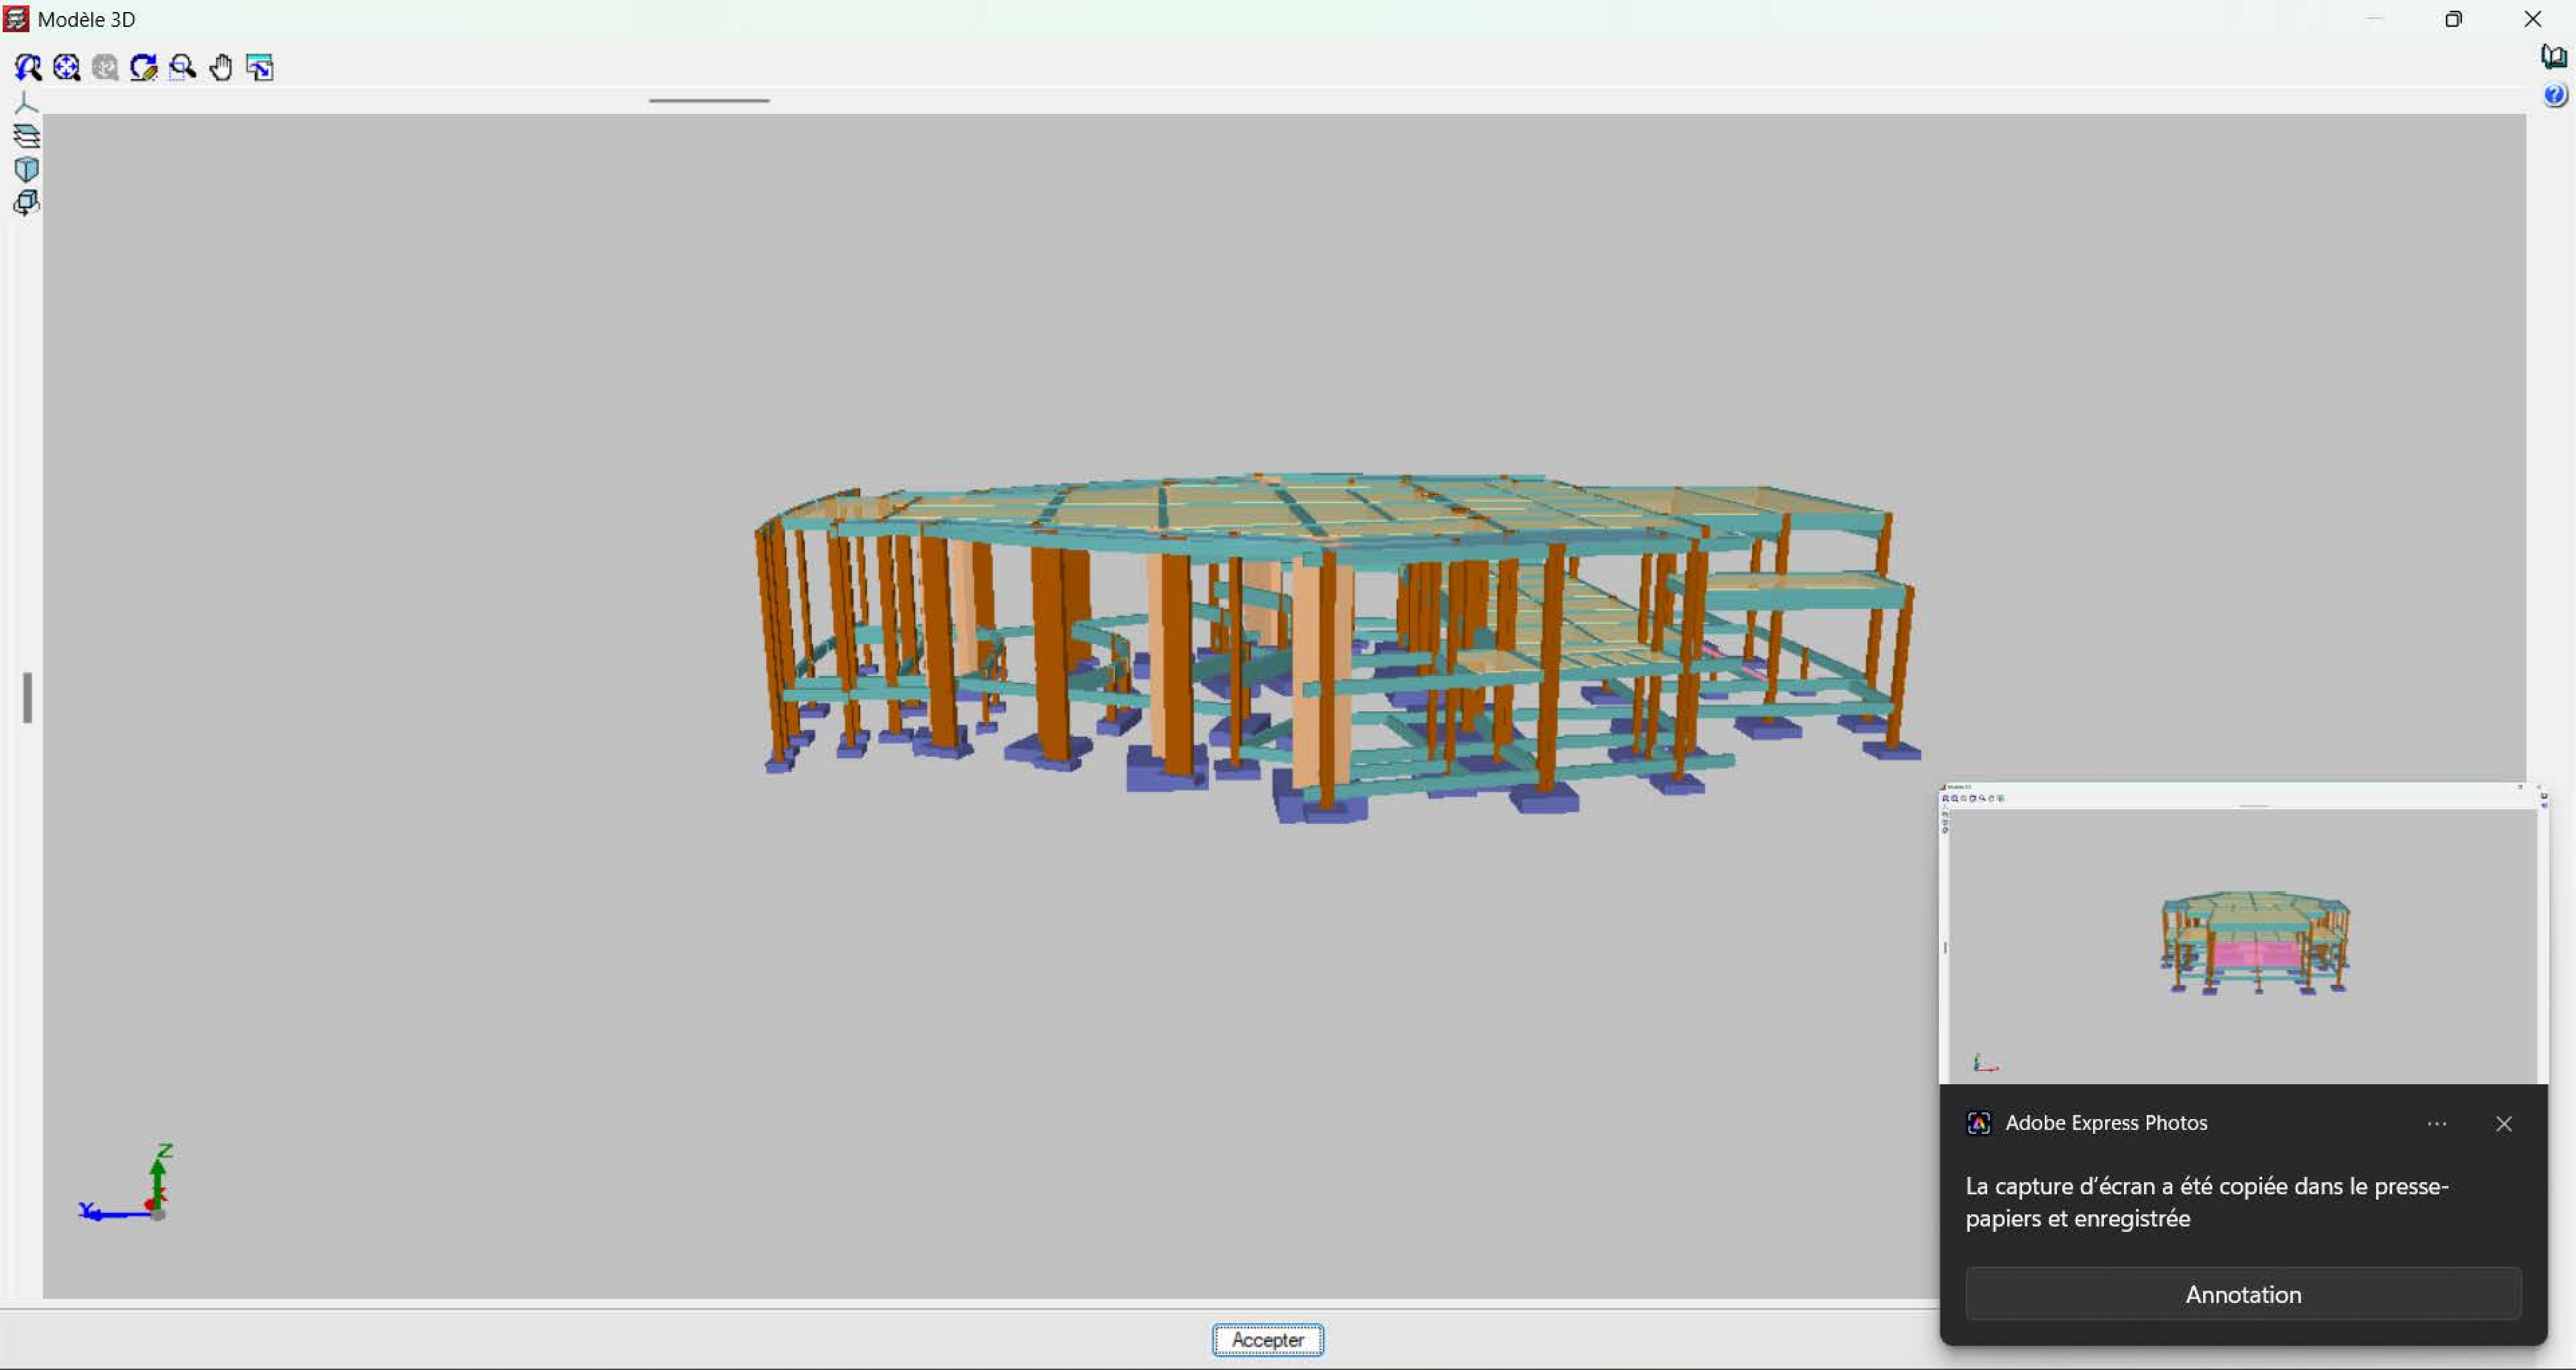
Modèle 3D
Z
Y
X
Accepter
Adobe Express Photos
Annotation

La capture d’écran a été copiée dans le presse-papiers et enregistrée

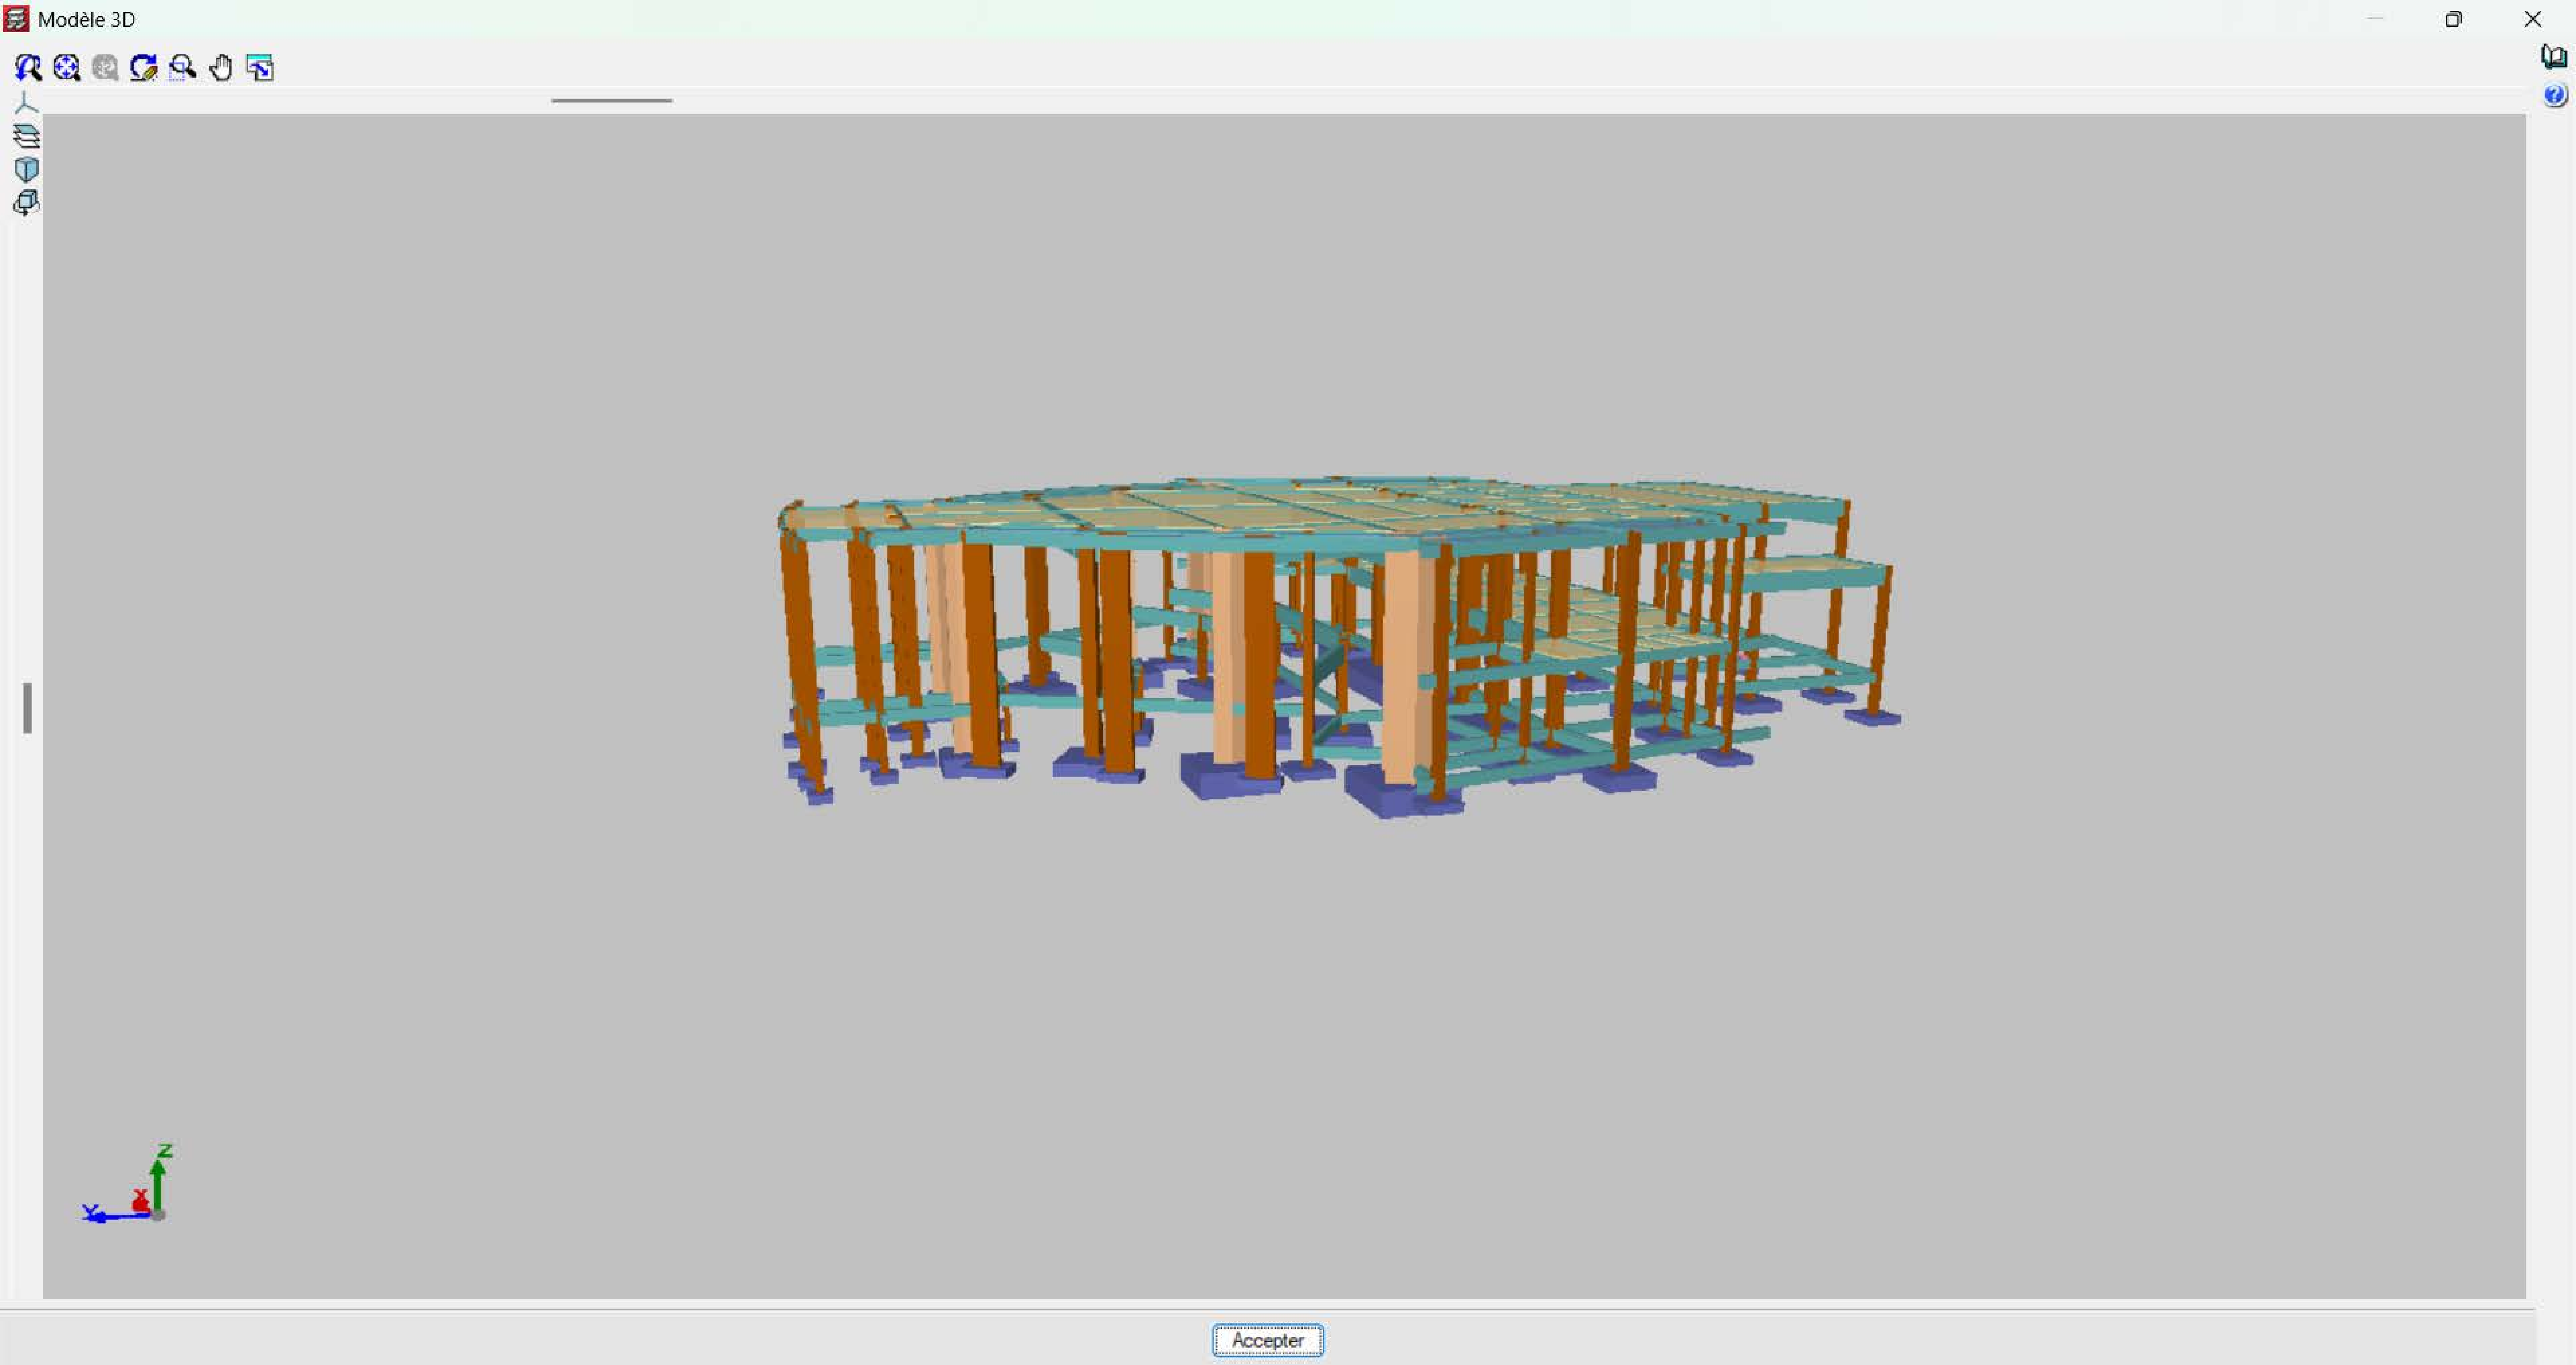
Modèle 3D
Z
X
Y
Accepter

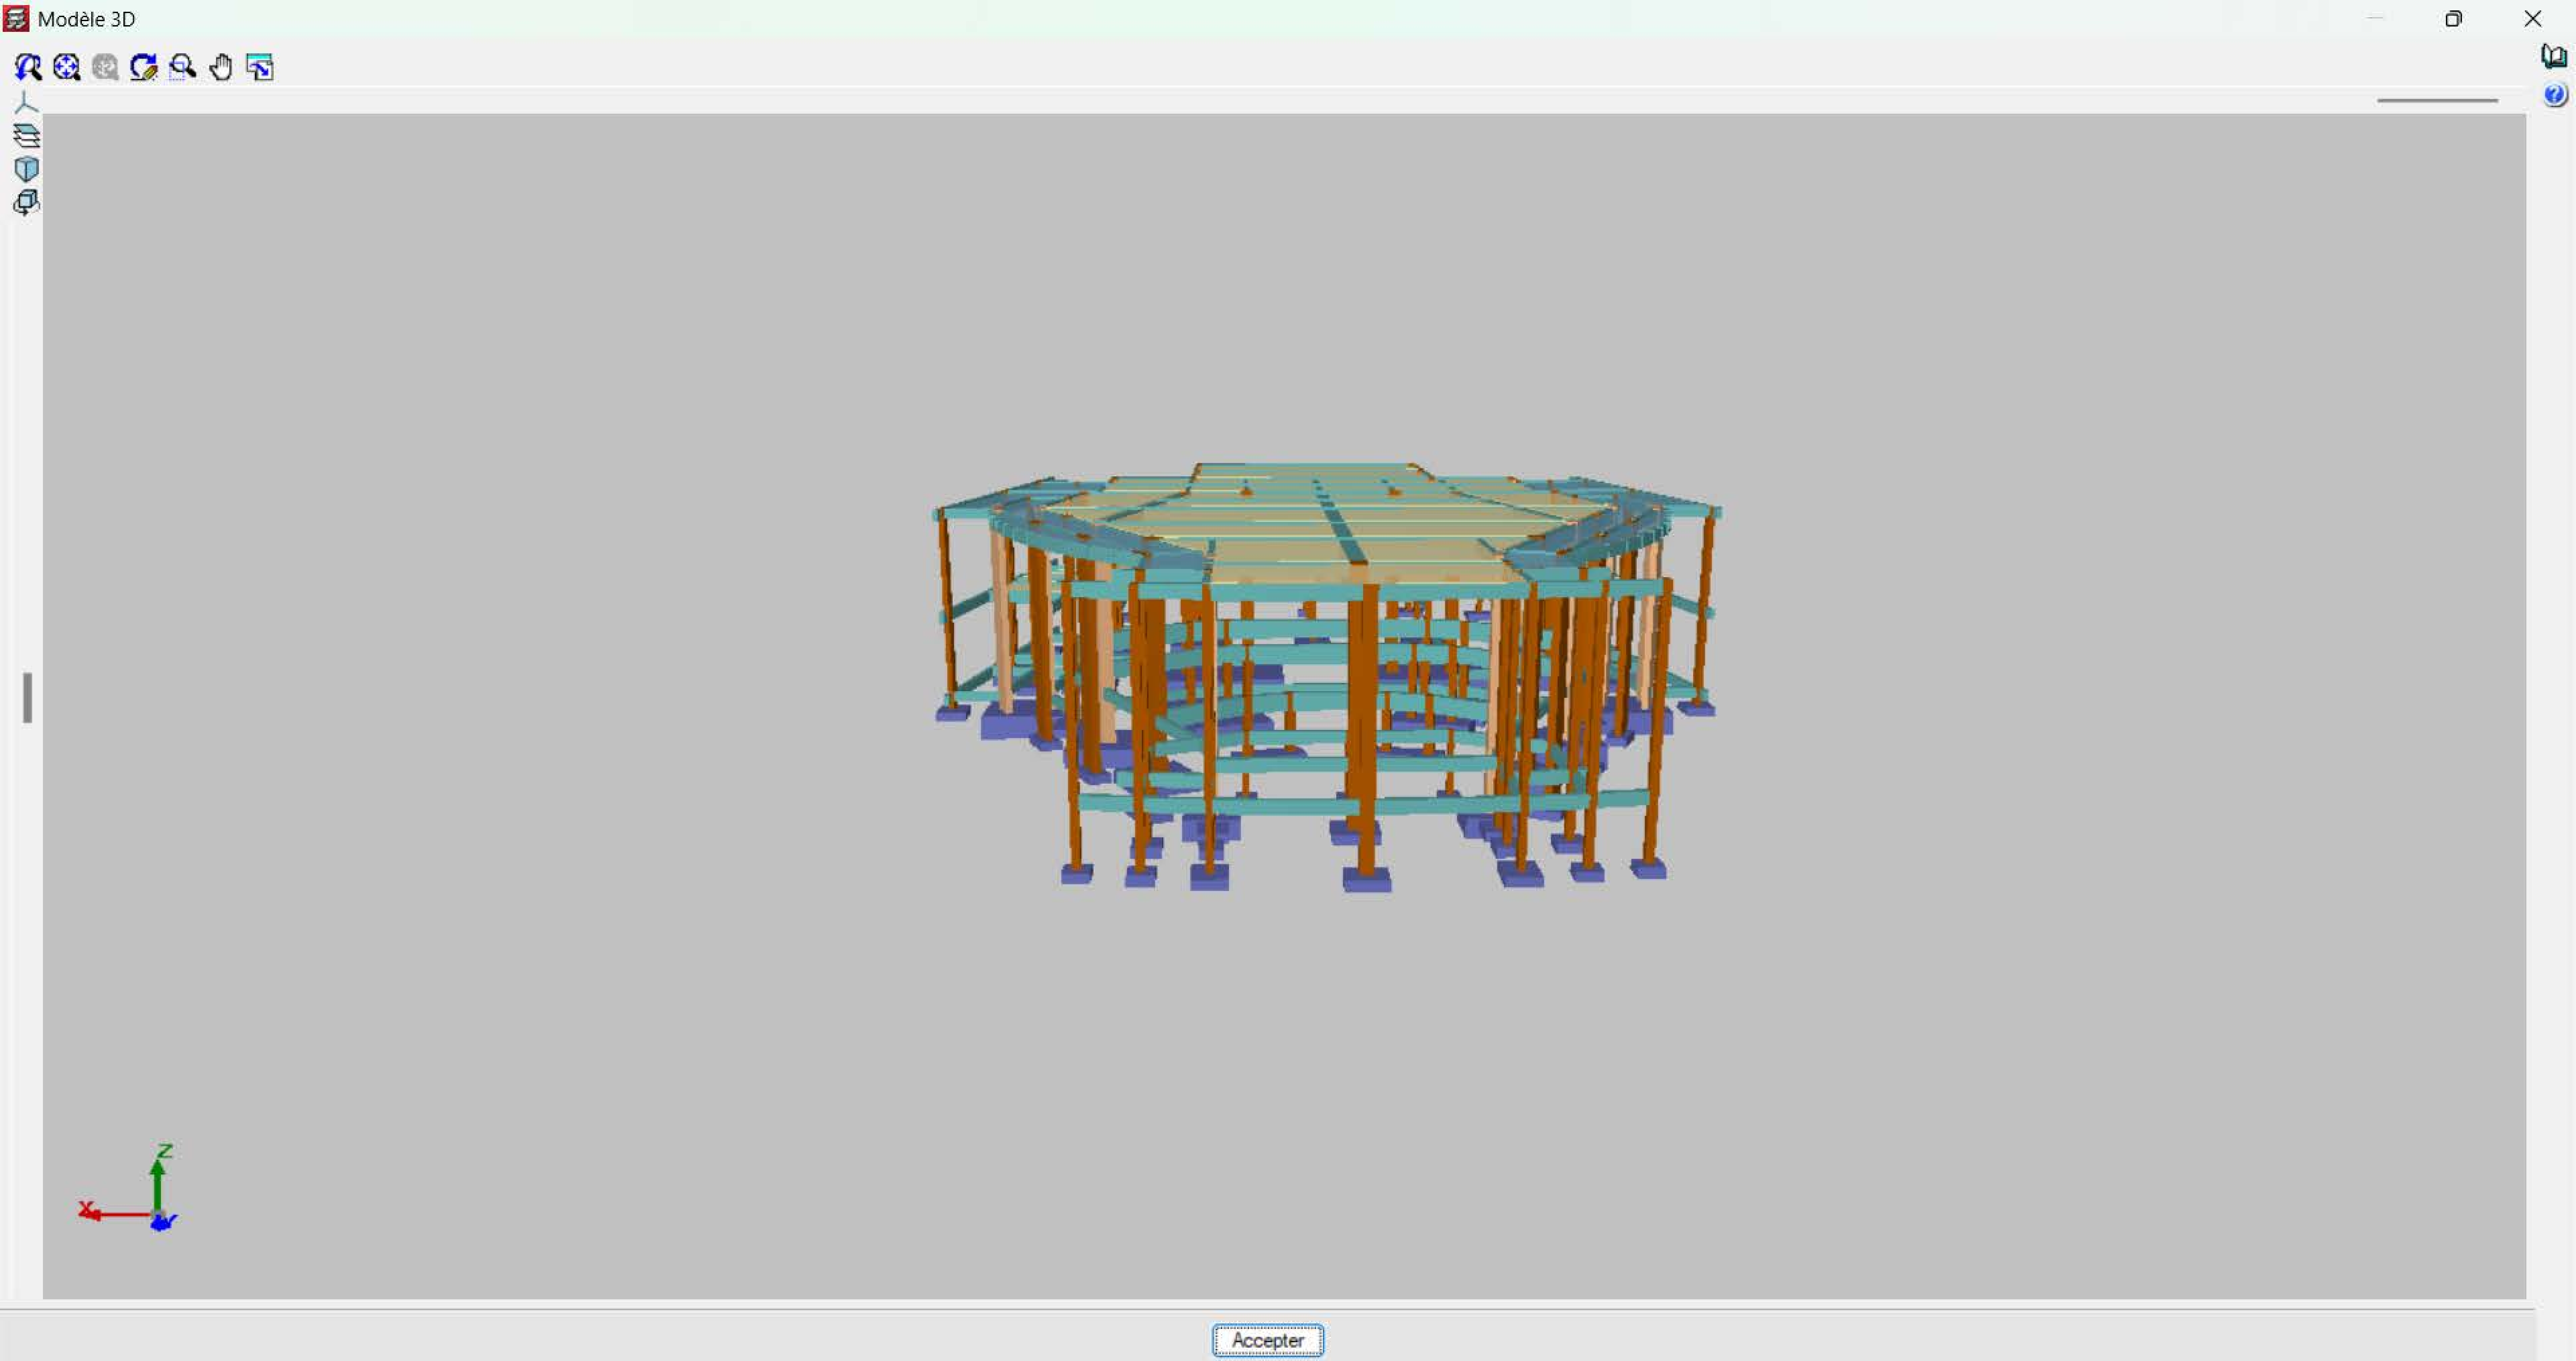
Modèle 3D
Z
X
Y
Accepter

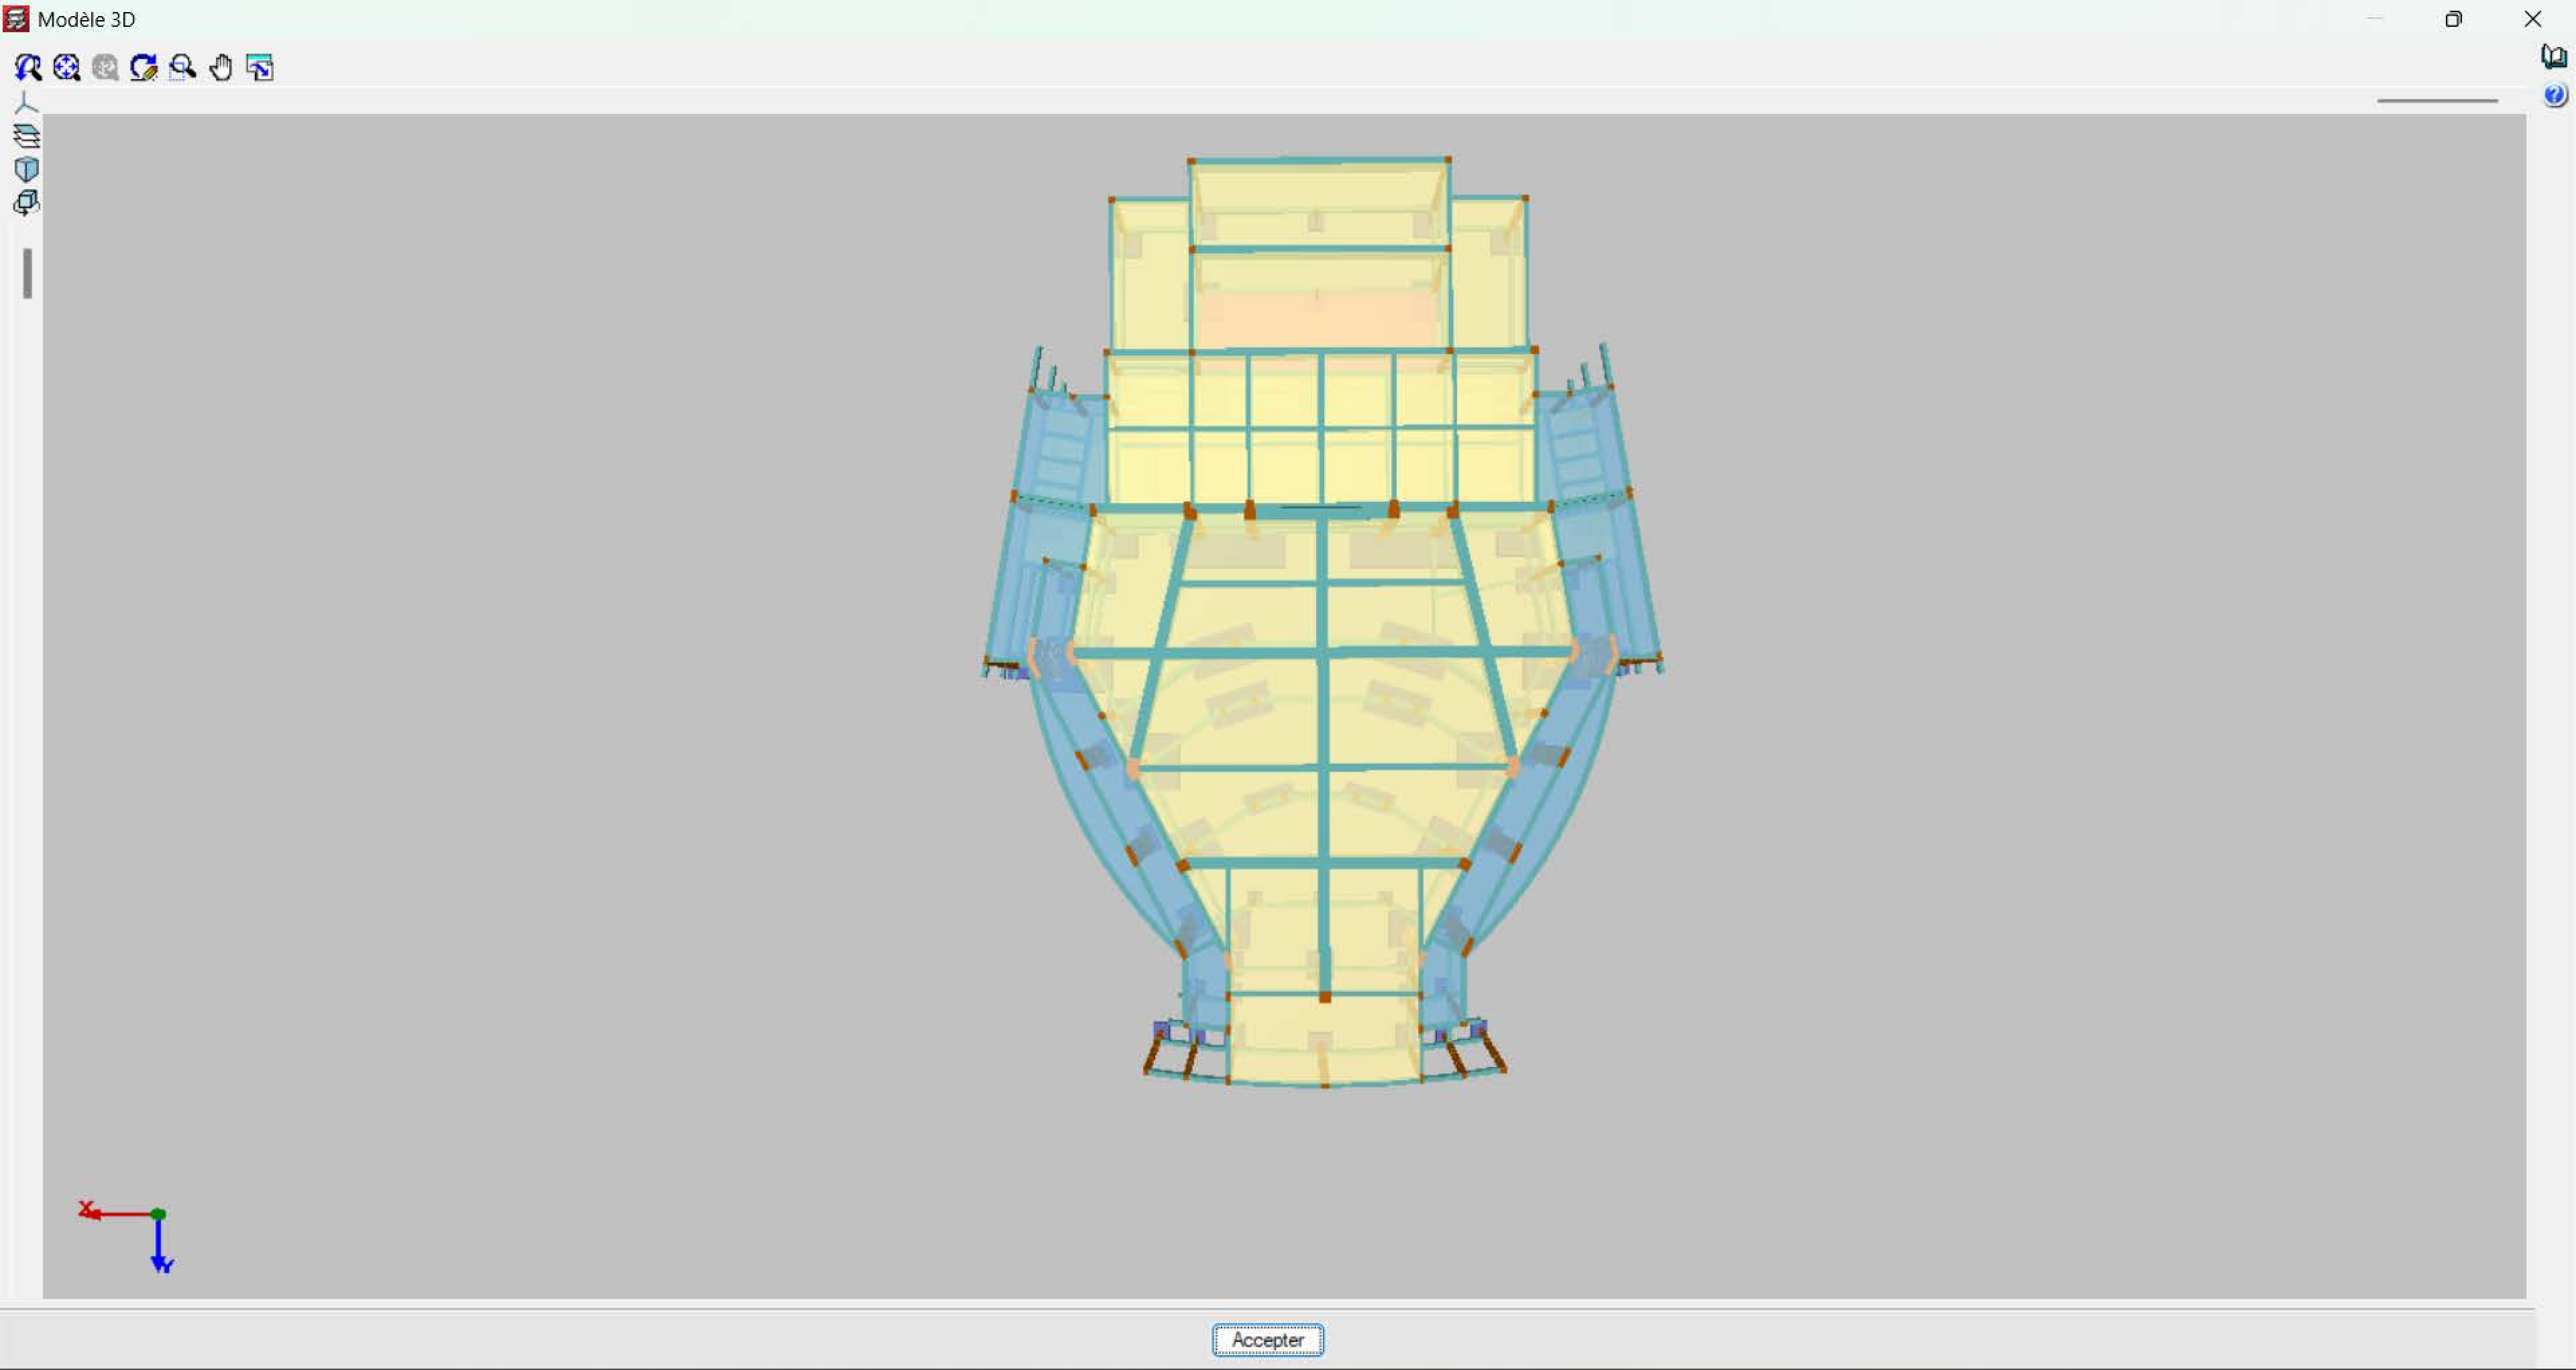

Modèle 3D
X
Y
Accepter