


TOUR TRANSPORTABLE

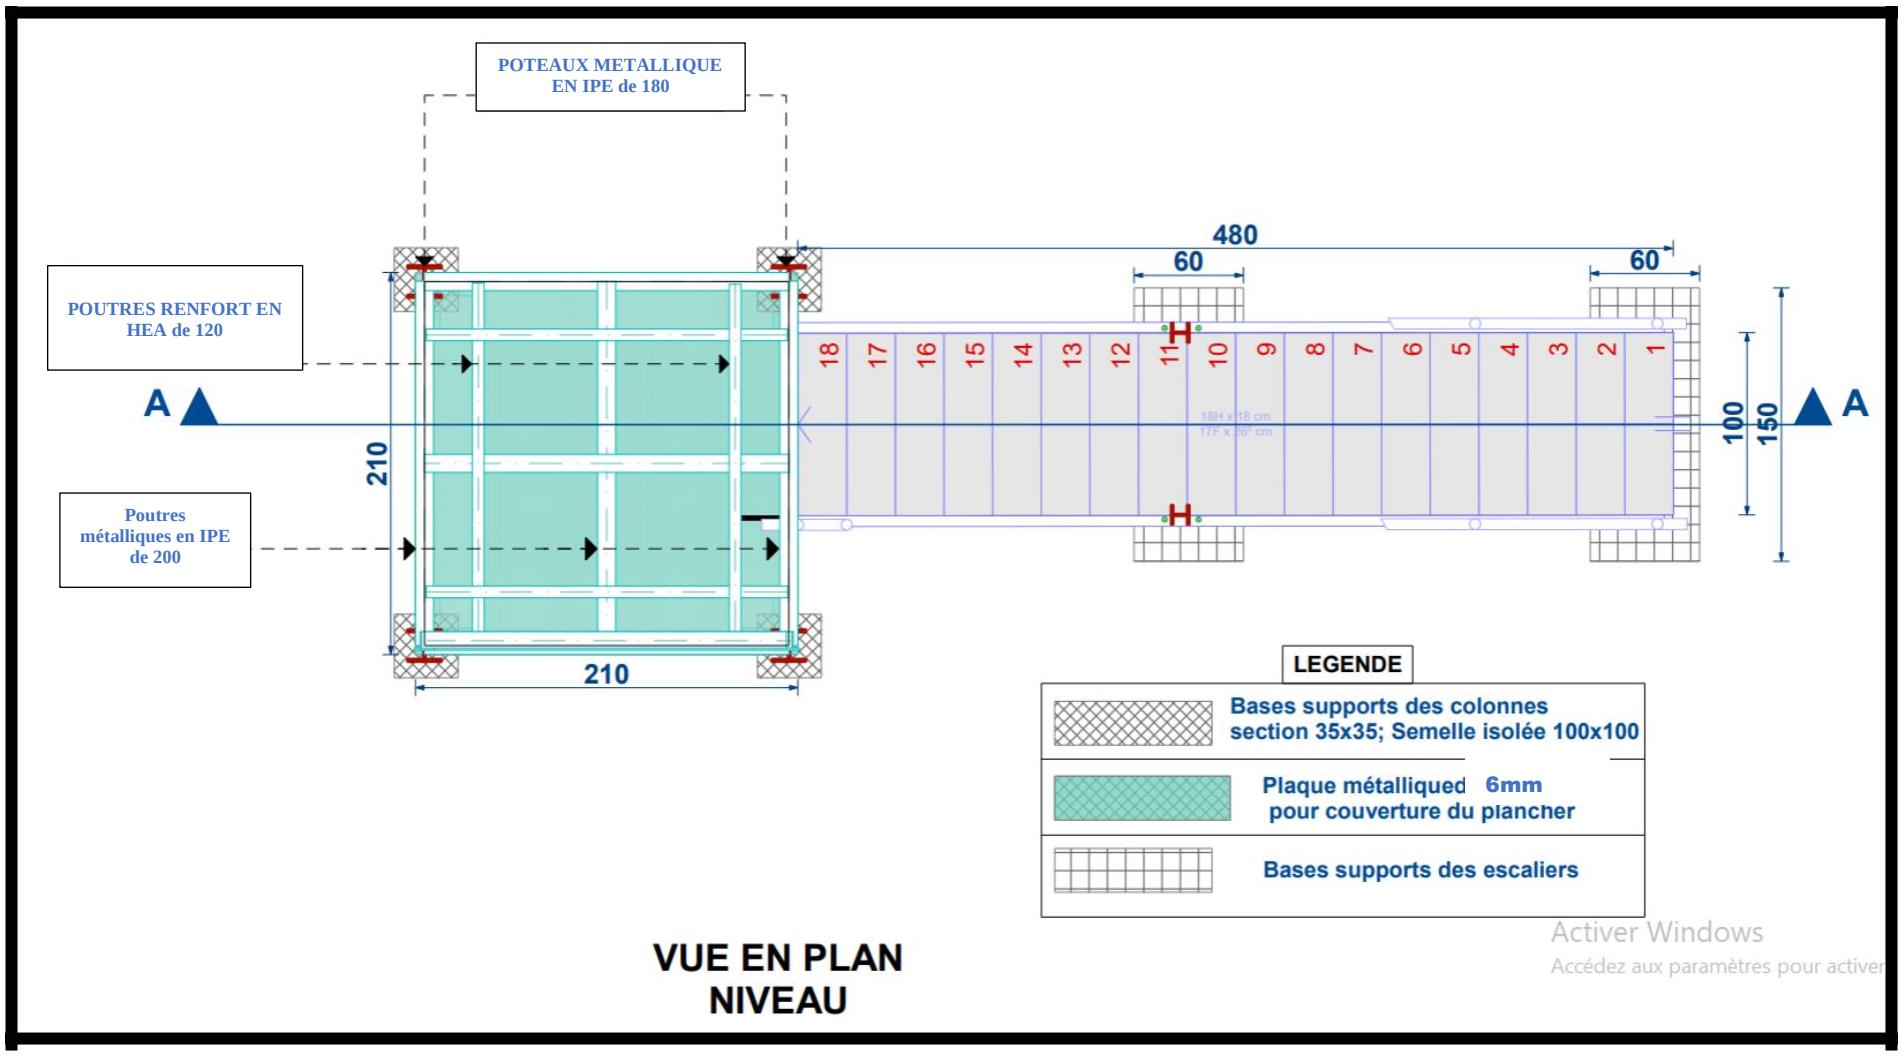

VUE EN PLAN NIVEAU

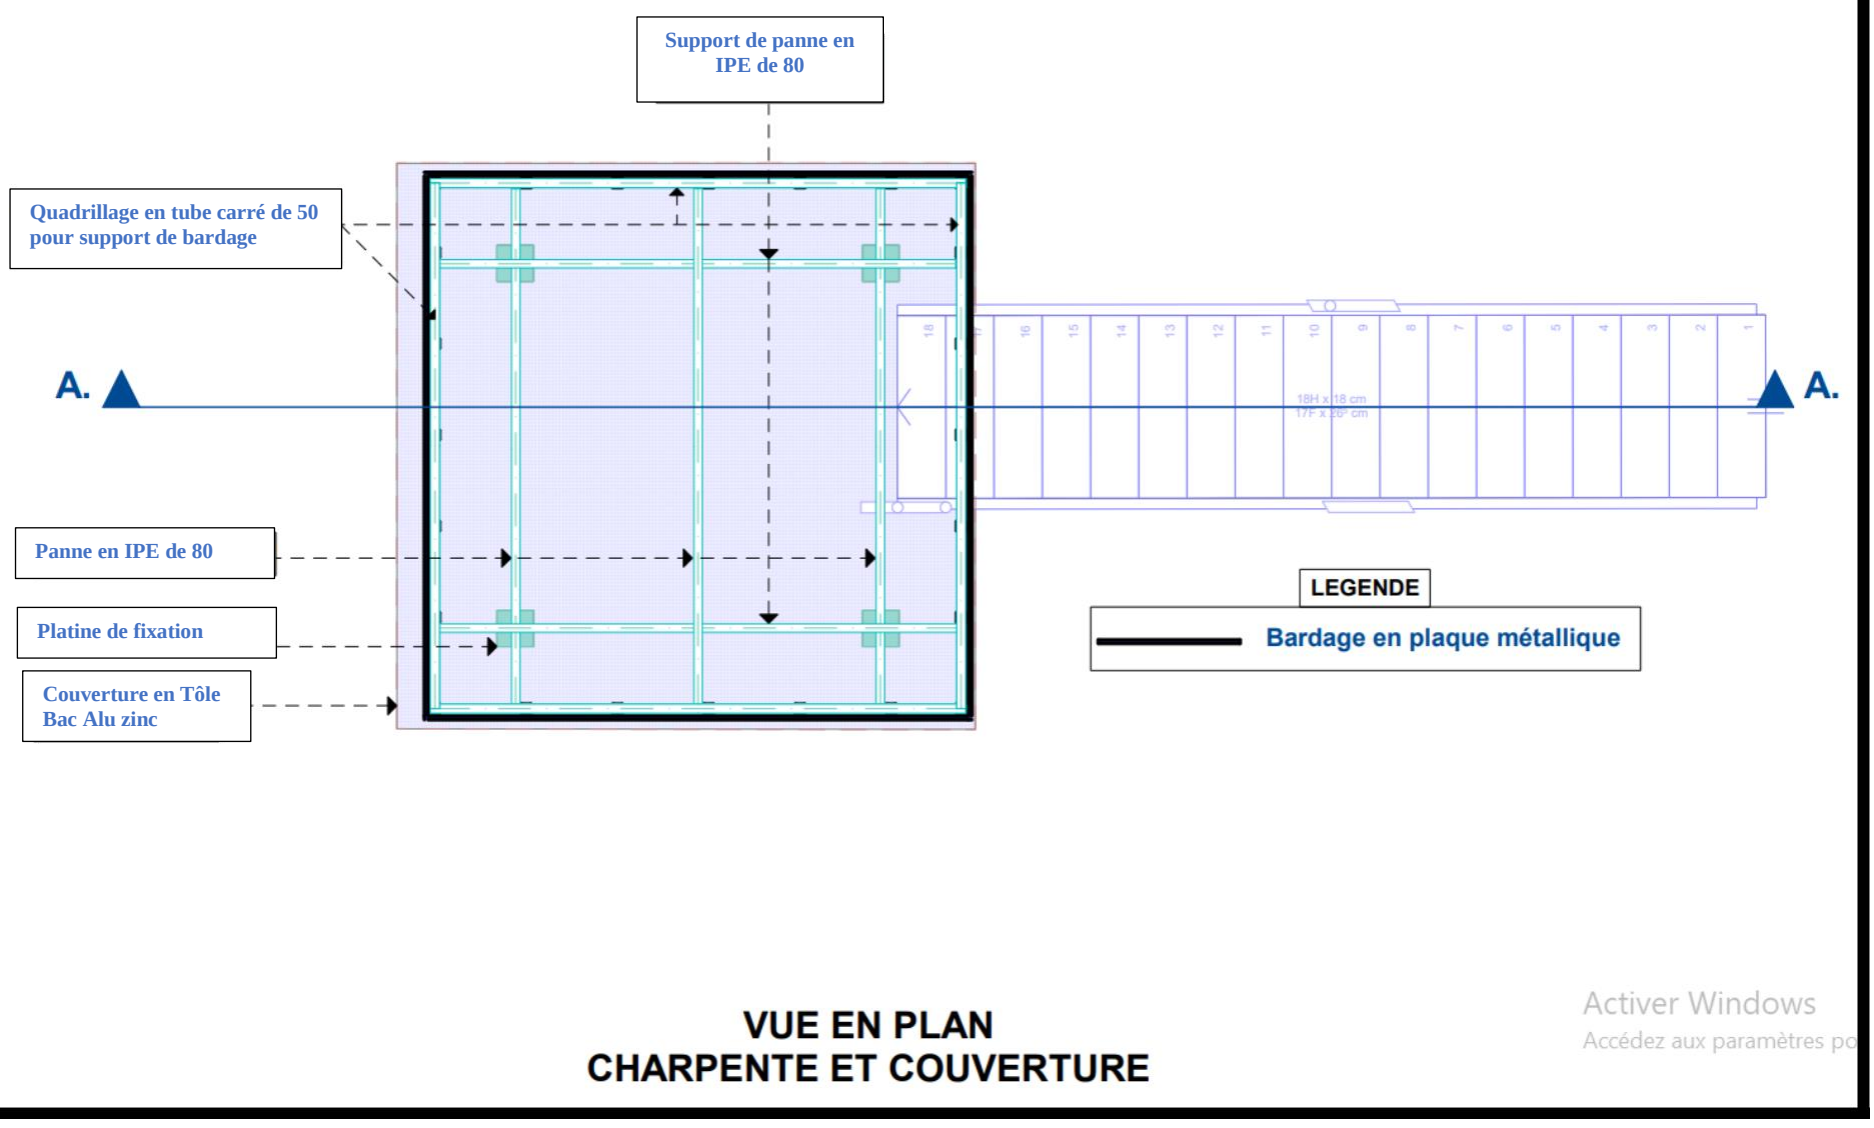

VUE EN PLAN CHARPENTE ET COUVERTURE

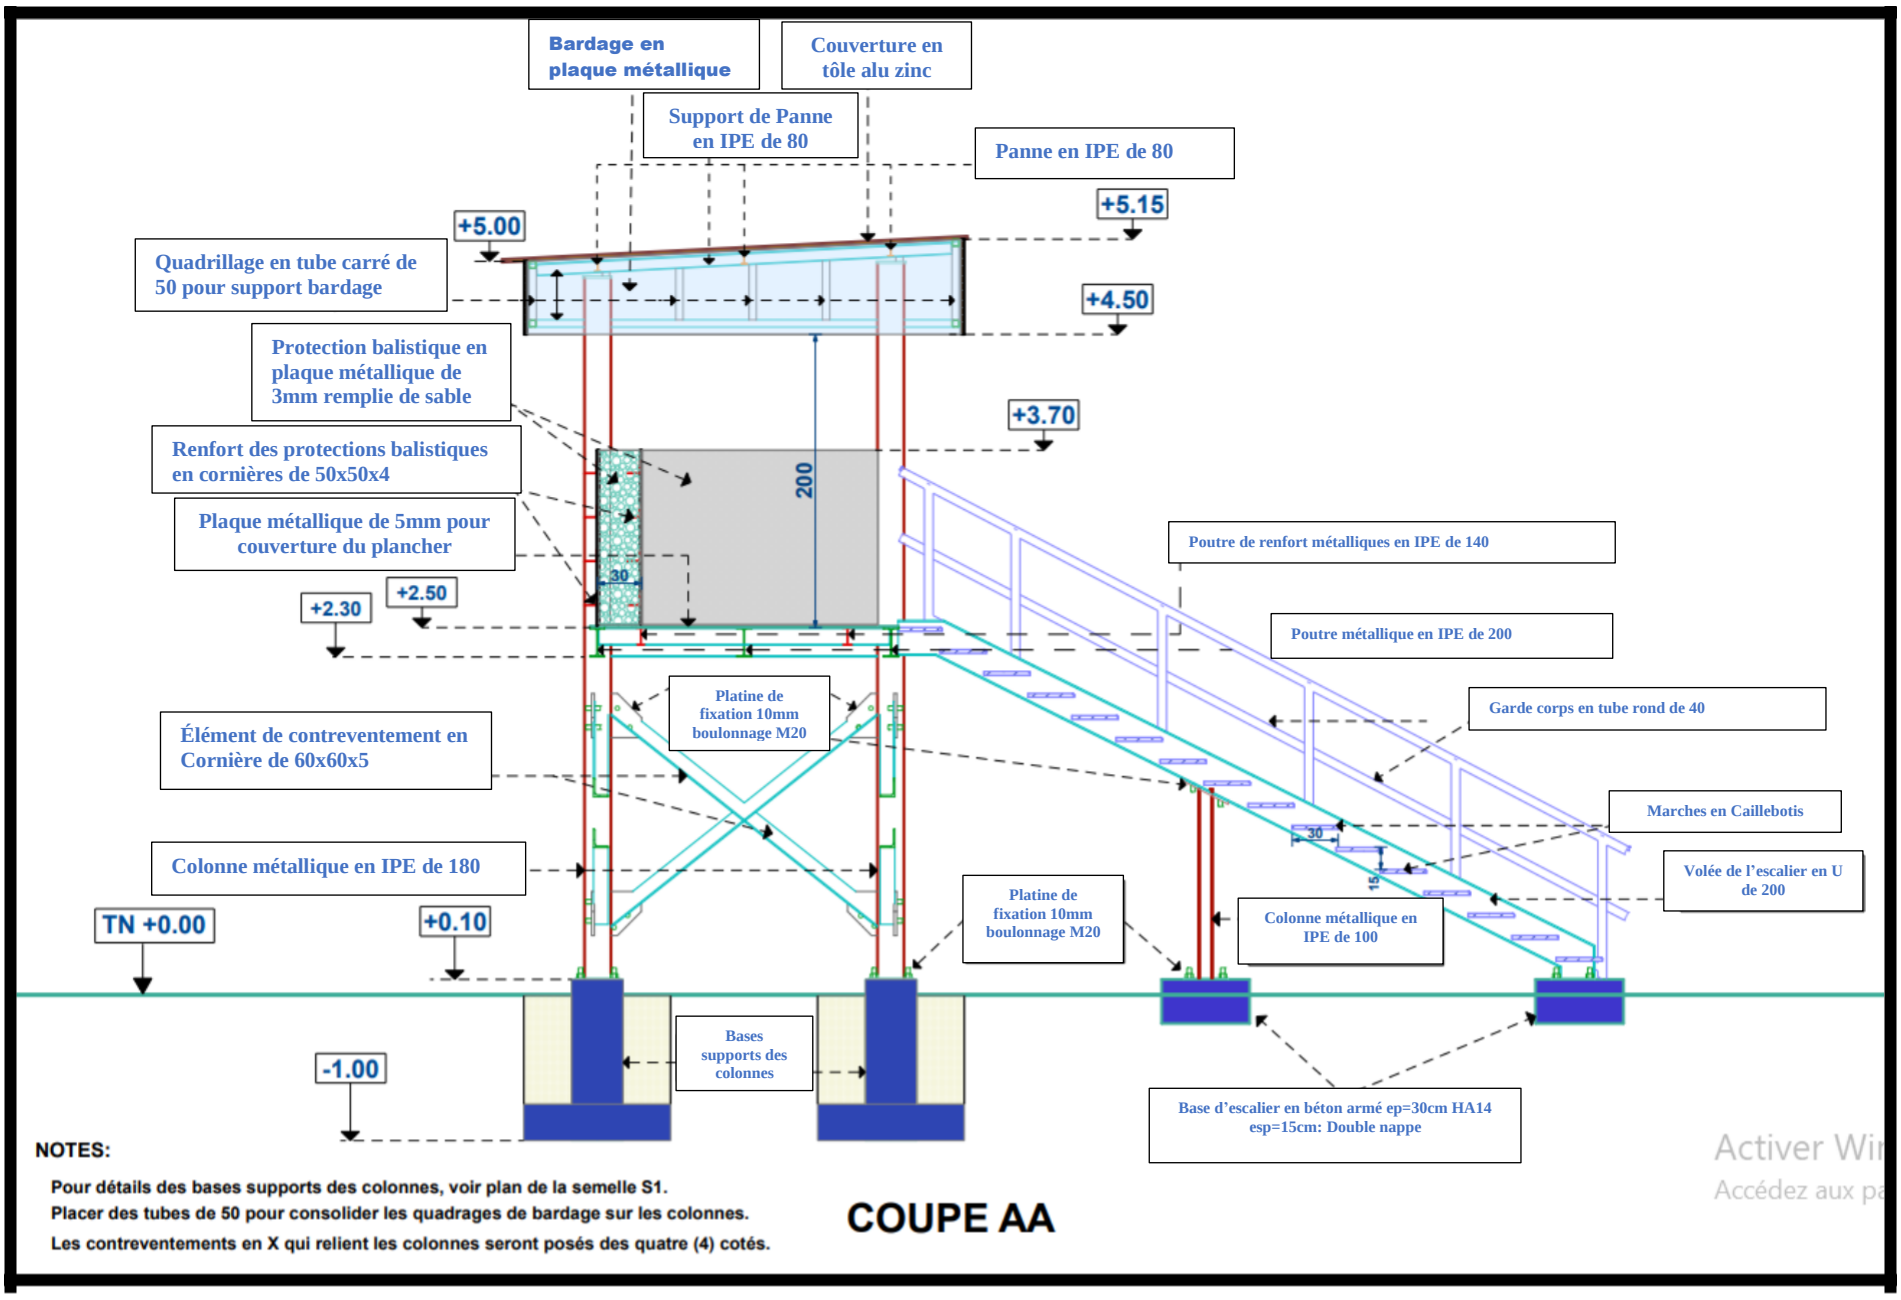


NOTES:


Pour détails des bases supports des colonnes, voir plan de la semelle S1.

Placer des tubes de 50 pour consolider les quadrages de bardage sur les colonnes.

Les contreventements en X qui relient les colonnes seront posés des quatre (4) cotés.

COUPE AA

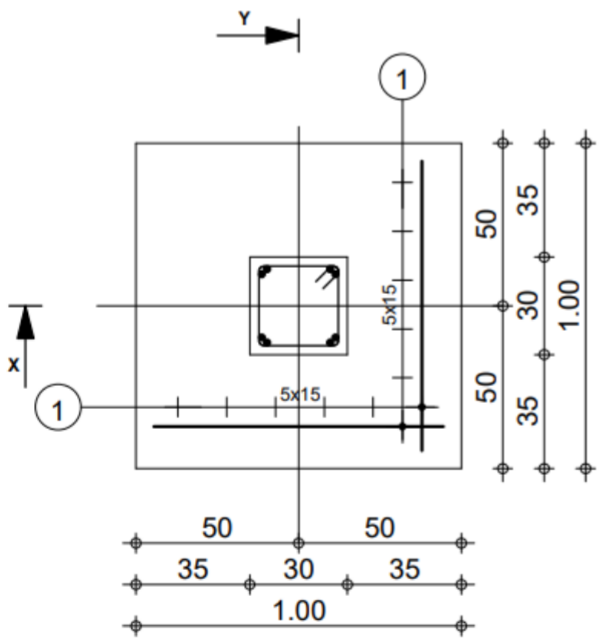

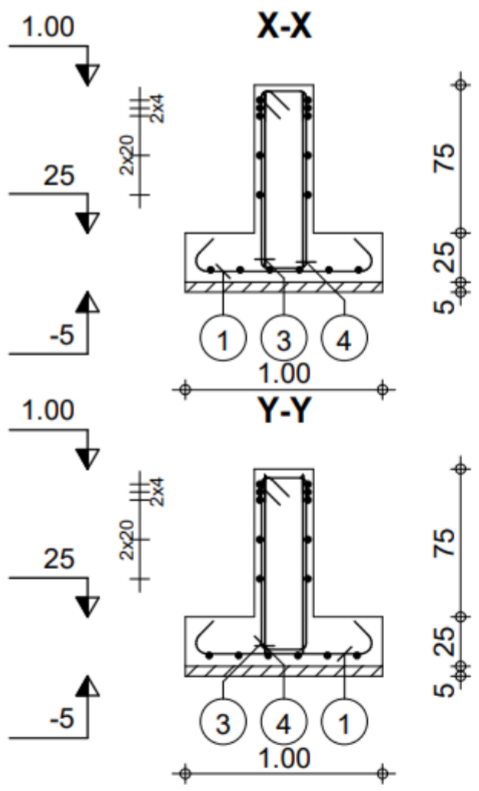

Pos.	Armature		Code	Forme	Pos.	Armature		Code	Forme
1	12HA 10	l=1.24	00	90	4	2HA 12	l=2.53	31	
2	5HA 6	l=1.12	31						
3	2HA 12	l=2.47	31						

Tél. Fax

Fissuration préjudiciable

Béton : C25/30 = 0.318 m3

Surface du coffrage = 1.9 m2

Densité = 60.69 kg/ m3

Acier HA 400 = 9.17 kg

Acier HA 400 = 10.1 kg

Enrobage c1 = 5 cm, c2 = 2.5 cm

Echelle pour la vue 1/20

S1

Nombre 1

TOUR MOBILE



